

STRUCTURAL NOTES

BUILDER / CONTRACTOR IS RESPONSIBLE FOR ENSURING THAT PLANS AND SPECIFICATIONS COMPLY WITH APPLICABLE REQUIREMENTS OF ANY GOVERNING BUILDING AUTHORITY.

METAL BUILDING STRUCTURE DESIGNED PER THE FOLLOWING LOADS:

CODE:IBC 21 I
WIND (MPH):115
EXPOSURE:C
ROOF SNOW LOAD (PSF):20.40
GROUND SNOW LOAD (PSF): 35
COLLATERAL LOAD (PSF):0.50
SEISMIC: 0.270
SEISMIC ZONE:D
THERMAL COEFFICIENT:1.20

DESIGN LOADS DESIGNATED WITHIN CONTRACT AND DRAWINGS DO NOT ALLOW FOR ANY TYPE OF OVERSTRESS, SUSTAINED, SHOCK, VIBRATION, DUCT WORK, PIPING, ETC.) SUSPENSION OF ANY LOAD INDUCING SYSTEM IS EXPLICITLY PROHIBITED UNLESS A CORRESPONDING REDUCTION IN CERTIFIED LIVE/SNOW LOADS CAN BE PERMITTED BY CODE.

DESIGN AND SPECIFICATION OF BASE STEEL TO CONCRETE SLAB ANCHORING IS NOT THE RESPONSIBILITY OF THE BUILDING MANUFACTURER.

BUILDING MANUFACTURER ASSUMES NO RESPONSIBILITY FOR CONCRETE SLAB FOUNDATION DESIGN, THICKNESS, MATERIALS, SITE SOIL CONDITIONS OR OTHER CONCRETE/MASONRY CONSTRUCTION.

ALL STRUCTURAL CONNECTIONS ARE TO BE MADE PER FASTENING DETAILS PRESENTED HEREIN. ALL STEEL FRAMING AND SHEETING MATERIALS MUST BE INSTALLED TO VERTICAL PLUMB AND HORIZONTALLY LEVEL.

THE BUILDING MANUFACTURER AND THE PROFESSIONAL ENGINEER SEALING THESE DRAWINGS ARE NOT THE PROFESSIONAL ENGINEER OF RECORD FOR THE ENTIRE PROJECT. THE PROFESSIONAL ENGINEER'S SEAL PERTAINS ONLY TO THE STRUCTURAL DESIGN OF THE METAL BUILDING SYSTEM; IT DOES NOT APPLY TO THE FOUNDATION SYSTEM, MASONRY DESIGN OR ANY OTHER ASPECT OF THE PROJECT UNLESS SPECIFICALLY STATED IN THESE DOCUMENTS.

BUILDING MANUFACTURER ASSUMES NO RESPONSIBILITY FOR ANY LOADS TO STRUCTURE NOT INDICATED AT THE TIME OF PURCHASE. ANY ALTERATIONS TO THE STRUCTURAL SYSTEM, REMOVAL OF ANY PART OF THE STRUCTURE OR REDUCTION IN THE STRENGTH OF THE STRUCTURAL MATERIALS OR LOADS MUST BE DONE UNDER THE DIRECTION OF REGISTERED ARCHITECT, CIVIL OR STRUCTURAL ENGINEER.

ALL CONCRETE AND MASONRY CONSTRUCTION MUST BE FLAT, LEVEL AND SQUARE PER THE SLAB PLAN DIMENSIONS HEREIN.

ALL JOBSITE DIMENSIONS AND CONDITIONS SHALL BE FIELD VERIFIED BEFORE ERECTION OF BUILDING STRUCTURE.

ALL OMISSIONS, CONFLICTS AND DISCREPANCIES SHALL BE REPORTED TO THE BUILDING MANUFACTURER BEFORE PROCEEDING WITH PROJECT WORK.

ALL TEMPORARY SUPPORTS, SUCH AS GUYS, BRACES, FALSWORK, CROWBARS, WINDBRACES OR OTHER ELEMENTS REQUIRED FOR SUCH GUYS, ERECTION ARE TO BE DETERMINED BY AND SUPPLIED BY BUILDER/CONTRACTOR.

BUILDING MANUFACTURER HAS MADE A COMMITMENT TO MANUFACTURE QUALITY BUILDING COMPONENTS THAT CAN BE SAFELY ERECTED, JOBSITE SITE SAFETY INSURANCE, SAFETY EQUIPMENT AND CONDITIONS ARE THE RESPONSIBILITY OF THE BUILDER/CONTRACTOR.

ALL COMPONENTS SHIPPED SHALL BE THOROUGHLY INSPECTED AND ACCOUNTED FOR AT THE TIME OF DELIVERY. ALL MATERIAL SHORTAGES OR DEFECTS MUST BE REPORTED WITHIN FIVE (5) WORKING DAYS OF MATERIAL DELIVERY TO THE BUILDING MANUFACTURER.

DIAPHRAGM ACTION OF THE METAL PANELS AT INTERIOR PARTITION WALLS IS UTILIZED FOR THE STABILITY OF THIS BUILDING. ANY MODIFICATION OR UNAUTHORIZED CUTTING OF INTERIOR PARTITION PANELS IS EXPRESSLY PROHIBITED BY THE BUILDING MANUFACTURER.

PARTITION PANELS HAVE BEEN SUPPLIED TO REACH ROOF LINE. THE TOP PARTITION PANEL CAN BE NOTCHED TO MATCH ROOF LINE AND CLEAR PURLIN LUG TO CLOSE IN THE UNIT AS DESIRED.

FIELD CUTTING OF STRUCTURAL, SHEETING AND TRIMS FOR SPLICE AND FINAL FITTING OF COMPONENTS IS REQUIRED PANELS.

ALL ROOF PANELS SHALL BE SEALED WITH 3/8" (MINIMUM) WIDTH MASTIC TAPE AS PROVIDED FOR PROJECT. ALL SHEET PROFILE FOAM CLOSURES AT EAVE, WALL AND RIDGE CONDITIONS AS PROVIDED FOR PROJECT MUST BE INSTALLED AS SHOWN HEREIN.

WALL PANELS AND WALL TRIMS, AT INTERIOR AND EXTERIOR, ARE TO BE SET WITH 1/4" CLEARANCE ABOVE CONCRETE SURFACES AND AT ANY LOCATIONS WHICH MAY BE SUBJECTED TO CONTACT WITH STANDING WATER.

LAP ALL FLASHINGS 2" MINIMUM AND SEAL AS REQUIRED FOR WATER TIGHTNESS

ALLOW 1/4" TOLERANCE AT EACH END FOR PURLINS, HEADERS AND GIRTS.

[illegible][illegible]

(BA)	- B4216R 4 X 2 X 16GA. ANGLE (5.9)	- FLOOR BASE ANGLE
(BC)	- U42516Z 1/8 X 2 7/8 X 16GA. CHANNEL (9.9)	- FLOOR BASE CHANNEL
(CC)	- C4216R 4 X 2 X 16GA. ZEE (8.9)	- 4" COLUMN
(CD)	- C62516R 6 X 2 1/2 X 16GA. ZEE (11.9)	- 6" COLUMN
(CH)	- C4216R 4 X 2 X 16GA. ZEE (8.9)	- RIGID HEAD
(CI)	- C43516R 4 X 3 1/2 X 16GA. ZEE (11.9)	- RIGID HEAD
(DC)	- U4216R 4 1/8 X 2 3/8 X 16GA. CHANNEL (8.9)	- EAVE CHANNEL
(EE)	- E64316LR 4 X 6 X 3 X 16GA. STRUT (13.9)	- EAVE STRUT
(FC)	- AS MANUFACTURED	- FLOOR FLIP
(G)	- C4216R 4 X 2 X 16GA. ZEE (8.9)	- GIRT
(HA)	- B4216R 4 X 2 X 16GA. ANGLE (5.9)	- HALL TOP REINFORCE
(HB)	- C4216R 4 X 2 X 16GA. ZEE (8.9)	- HALL HEAD REINFORCEMENT
(JR)	- C62516R 6 X 2 1/2 X 16GA. ZEE (11.9)	- JACK Rafter
(J)	- M1216R 12 X 4 X 1 X 16GA. ZEE (20.9)	- MILLER
(MC)	- B4216R 4 X 2 X 2" LONG 16GA. ANGLE (5.9)	- MINI CUP
(PA)	- Z42516R 2 1/2 X 4 X 2 1/2 X 16GA. ZEE (9.9)	- PURGE PURLIN
(P)	- Z62516R 2 1/2 X 6 X 2 1/2 X 16GA. ZEE (11.9)	- PURGE PURLIN
(PB)	- Z82516R 2 1/2 X 8 X 2 1/2 X 16GA. ZEE (13.9)	- PURGE PURLIN
(PA)	- B4216R 4 X 2 X 16GA. ANGLE (5.9)	- PARTITION ANGLE
(BA)	- B4216R 4 X 2 X 16GA. ANGLE (5.9)	- RAKE ANGLE
(RS)	- E64316LR 4 X 6 X 3 X 16GA. STRUT (13.9)	- RIDGE STRUT

(ML) - 29GA. M-LOC WALL PANEL	(F1) - 1/2" X 2 3/4" CONC. EXPANSION ANCHOR	- BASE TO SLAB CONNECTIONS
(RL) - 29GA. R-LOC WALL PANEL	(F2) - 1/2" X 2 SELF-DRILLING TEK (PLTD)	- STRUCTURAL STEEL CONNECTIONS
(PL) - 29GA. PANEL-LOC WALL PANEL	(F3) - 1/2 X 1 SELF-DRILLING TEK (PLTD)	- PARTITION SHEETING
(RR) - 29GA. PBR ROOF PANEL	(F4) - 1/2 X 2 SELF-DRILLING TEK (PLTD)	- PARTITION ANGLE CONNECTIONS
(RW) - 29GA. PBR WALL PANEL	(F5) - 12 X 1 1/4 WASHER TEK (PTD)	- EXTERIOR WALL SHEETING
(CL) - 24GA. CENTRAL-LOC SSR 24" ROOF PANEL	(F6) - 12 X 1 1/4 WASHER ZAC (PTD)(PLTD)	- ROOF SHEETING
(CL-20) - SSR LOW FIXED CLIP	(F7) - 12 X 1 1/4 WASHER TEK (PTD)	- EXTERIOR TRIM DRILLER
	(F8) - 12 X 7/8 WASHER TEK (PTD)	- EXTERIOR WALL PANEL LAP
	(F9) - 12 X 7/8 WASHER ZAC (PTD)(PLTD)	- ROOF PANEL LAP
	(F10) - 12 X 7/8 WASHER TEK (PTD)	- EXTERIOR TRIM LAP
	(F11) - 1/8 POP RIVET	- EXTERIOR TRIM
	(F12) - 12 X 1 1/4 WASHER TEK (PTD)	- INTERIOR WALL SHEETING
	(F13) - 12 X 1 1/4 WASHER TEK (PTD)	- INTERIOR TRIM DRILLER
	(F14) - 12 X 7/8 WASHER TEK (PTD)	- INTERIOR WALL PANEL LAP
	(F15) - 12 X 7/8 WASHER TEK (PTD)(PLTD)	- INTERIOR TRIM LAP
	(F17) - 1/4"-14 X 1" SDS W/ WASHER #1(PTD)	- "CL" CLIP/STRUCTURE CONNECTIONS
	(F18) - 1/4"-14 X 1 1/4" SDS ZAC W/ WASHER #1(PTD)(PLTD)	- "CL" TRIM DRILLER
	(F19) - 1/4 X 7/8" SDS W/ WASHER #4(PTD)(PLTD)	- "CL" ROOF LAP
	(F20) - 1/4"-14 X 1 1/4" SDS ZAC W/ WASHER #1(PTD)(PLTD)	- "CL" TRIM DRILLER
	(F21) - 1/4 X 7/8" SDS ZAC W/ WASHER #4(PTD)(PLTD)	- "CL" TRIM LAP

(BTR)	= 7/8" ROLL MASTIC	(ICB)	= INSIDE CORNER BOX
(CLIN)	= R PANEL INSIDE FOAM CLOSURE	(JA)	= DOOR JAMB TRIM
(CLOUT)	= R PANEL OUTSIDE FOAM CLOSURE	(JC)	= DOOR JAMB COVER TRIM
(GECEL)	= GUTTER SEAL	(MC)	= DOOR MULLION COVER TRIM
(IN)	= R PANEL INSIDE CORNER TRIM	(OCB)	= OUTSIDE CORNER BOX
(OU)	= R PANEL OUTSIDE CORNER TRIM	(PB)	= PEAK BOX
(CM)	= DOOR CORNER MULLION TRIM	(REND)	= RAKE TRIM END CAP
(DK)	= DOWNSPOUT WITH KICK OUT	(RT)	= RAKE TRIM
(DSS)	= DOWNSPOUT STRAP	(TI)	= ROOF TIE IN TRIM
(EF)	= EAVE FLASHING	(TR)	= ROOF STEP TRANSITION FLASHING
(FRC)	= FORMED RIDGE CAP	(4SP)	= 4OZ. TOUCH UP SPRAY PAINT
(GE)	= GUTTER END CAP		
(GS)	= GUTTER HANGER STRAP		
(GU)	= GUTTER		
(HC)	= DOOR HEAD COVER TRIM		
(HE)	= DOOR HEAD TRIM		
(H)	= HIGH EAVE TRIM		
(HT)	= HALL TOP TRIM		

(BTR)	= 7/8" ROLL MASTIC	(ICB)	= INSIDE CORNER BOX
(CLIN)	= R PANEL INSIDE FOAM CLOSURE	(JA)	= DOOR JAMB TRIM
(CLOUT)	= R PANEL OUTSIDE FOAM CLOSURE	(JC)	= DOOR JAMB COVER TRIM
(GECEL)	= GUTTER SEAL	(MC)	= DOOR MULLION COVER TRIM
(IN)	= R PANEL INSIDE CORNER TRIM	(OCB)	= OUTSIDE CORNER BOX
(OU)	= R PANEL OUTSIDE CORNER TRIM	(PB)	= PEAK BOX
(CM)	= DOOR CORNER MULLION TRIM	(REND)	= RAKE TRIM END CAP
(DK)	= DOWNSPOUT WITH KICK OUT	(RT)	= RAKE TRIM
(DSS)	= DOWNSPOUT STRAP	(TI)	= ROOF TIE IN TRIM
(EF)	= EAVE FLASHING	(TR)	= ROOF STEP TRANSITION FLASHING
(FRC)	= FORMED RIDGE CAP	(4SP)	= 4OZ. TOUCH UP SPRAY PAINT
(GE)	= GUTTER END CAP		
(GS)	= GUTTER HANGER STRAP		
(GU)	= GUTTER		
(HC)	= DOOR HEAD COVER TRIM		
(HE)	= DOOR HEAD TRIM		
(H)	= HIGH EAVE TRIM		
(HT)	= HALL TOP TRIM		



FOR APPROVAL ONLY
NOT FOR CONSTRUCTION

ERECTOR NOTE:
A DETAILED INSTALLATION GUIDE IS AVAILABLE AND SHOULD BE
CONSULTED DURING THE ERECTION OF THIS BUILDING PACKAGE.
PLEASE CONTACT US IF YOU HAVE NOT RECEIVED A COPY OF
THE INSTALLATION GUIDE AND ONE WILL BE PROVIDED TO YOU.

THESE DRAWINGS ARE THE SOLE AND EXCLUSIVE PROPERTY OF THE BUILDING MANUFACTURER, SENSITIVE, UNPUBLISHED, AND CONFIDENTIAL INFORMATION CONTAINED HEREIN IS NOT TO BE DISCLOSED OR USED, IN WHOLE OR IN PART, FOR ANY PURPOSES OTHER THAN TO BENEFIT THE PERSONS TO WHOM THESE DRAWINGS TO UNAUTHORIZED PERSONS IS STRICTLY PROHIBITED. THESE DRAWINGS MAY NOT BE USED TO CONSTRUCT LIKE PROJECTS WITHOUT WRITTEN PERMISSION FROM THE BUILDING MANUFACTURER. THIS DOCUMENT AND ALL COPIES MUST BE RETURNED UPON DEMAND.

PROJECT: BW62 Begghner April 2026

SIZE: 30.0 x 150.0 x 8.5

CITY: Lenoir City

STATE: TN


ROI Metal Buildings

423-991-0130


JOB ID: 94095

Sheet


E1

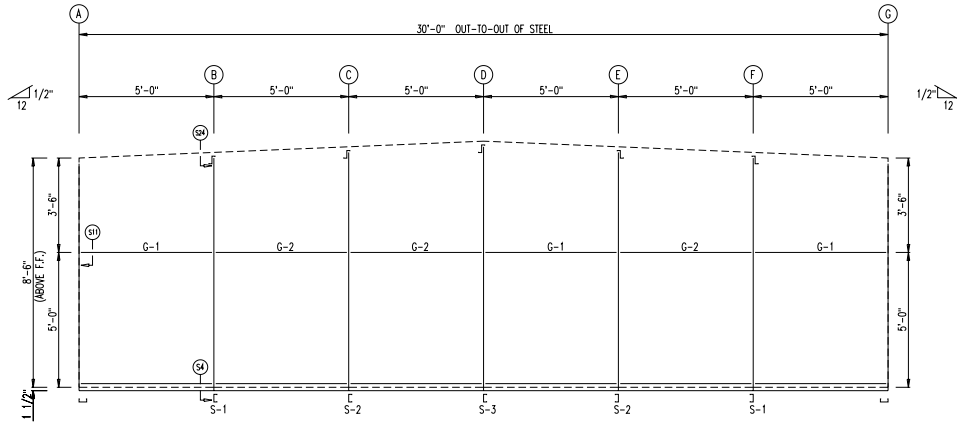


ENDWALL FRAMING FRAME LINE: 1

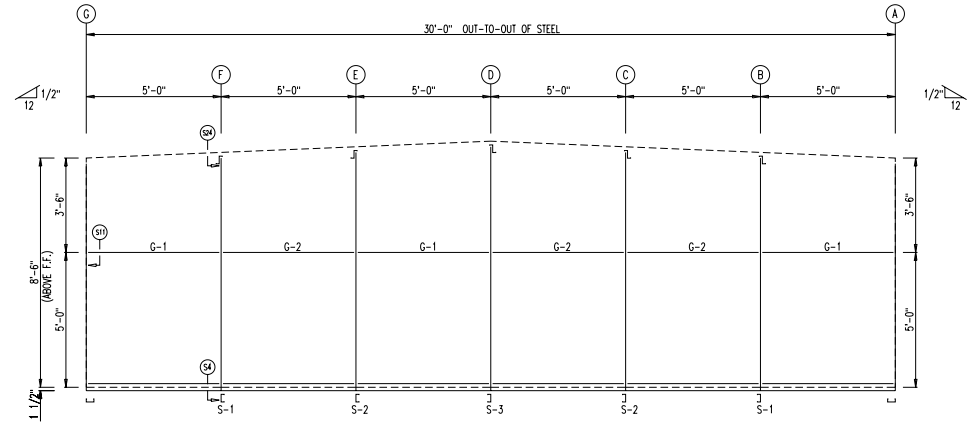

ENDWALL FRAMING FRAME LINE: 31

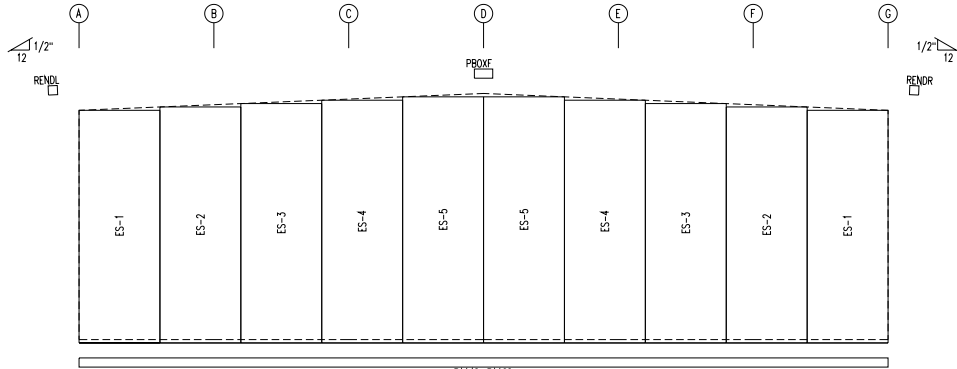

ENDWALL SHEETING & TRIM FRAME LINE: 1
PANELS: 26 Ga. RL - NEED COLOR

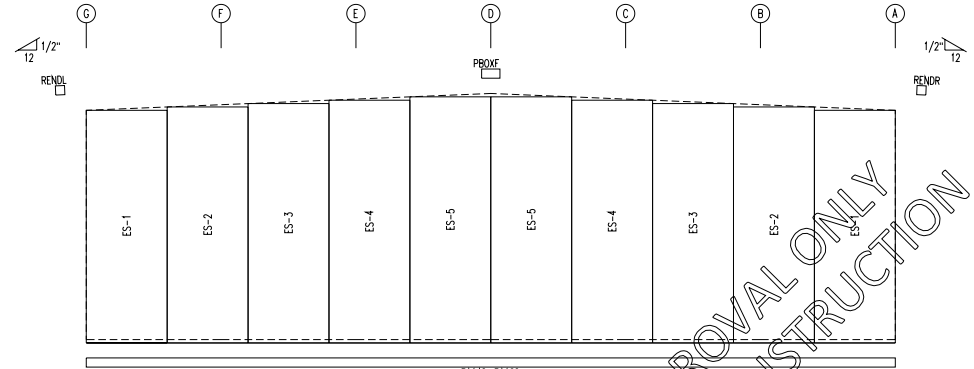

ENDWALL SHEETING & TRIM FRAME LINE: 31
PANELS: 26 Ga. RL - NEED COLOR

FOR APPROVAL ONLY
NOT FOR CONSTRUCTION

CONFIDENTIAL AND PROPRIETARY INFORMATION
THESE DRAWINGS ARE THE SOLE AND EXCLUSIVE PROPERTY OF THE BUILDING MANUFACTURER. SENSITIVE INFORMATION IS CONTAINED HEREIN. NO PART OF THESE DRAWINGS MAY BE USED FOR ITS REPRODUCTION OR TRANSMISSION IN ANY FORM OR BY ANY MEANS, ELECTRONIC OR MECHANICAL, INCLUDING PHOTOCOPYING, RECORDING, OR BY ANY INFORMATION STORAGE AND RETRIEVAL SYSTEM, WITHOUT THE WRITTEN PERMISSION OF THE BUILDING MANUFACTURER. THESE DRAWINGS MAY NOT BE USED TO CONSTRUCT ANY BUILDING WITHOUT THE WRITTEN PERMISSION OF THE BUILDING MANUFACTURER. THIS DOCUMENT AND ALL COPIES MUST BE RETURNED UPON DEMAND.

PROJECT: BWA26090ner April 2026
SIZE: 30.0 x 150.0 x 8.5
CITY: Lenoir City
STATE: TN



ROI Metal Buildings
423-991-0130

JOB ID: 94095

Sheet

F2

APPROVAL	PRINTS ISSUED FOR	BY	DATE
			5/6/26

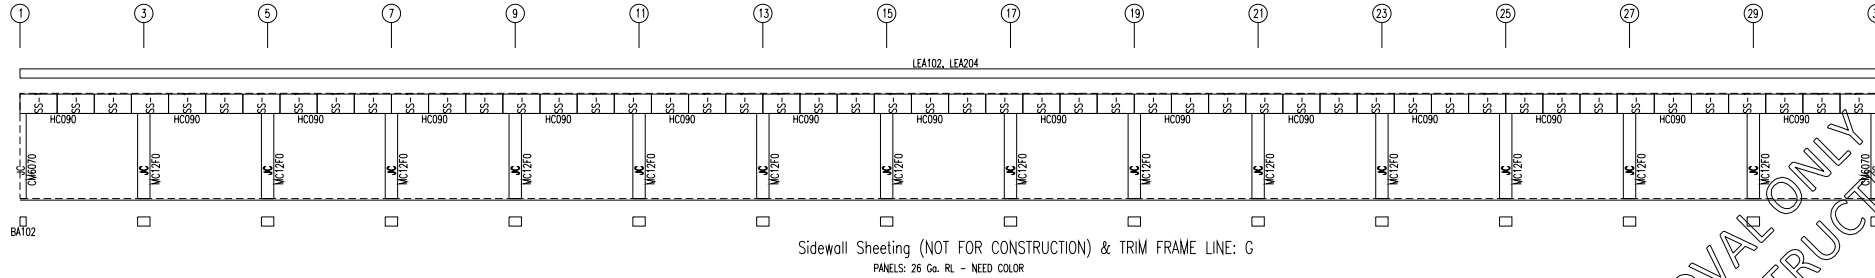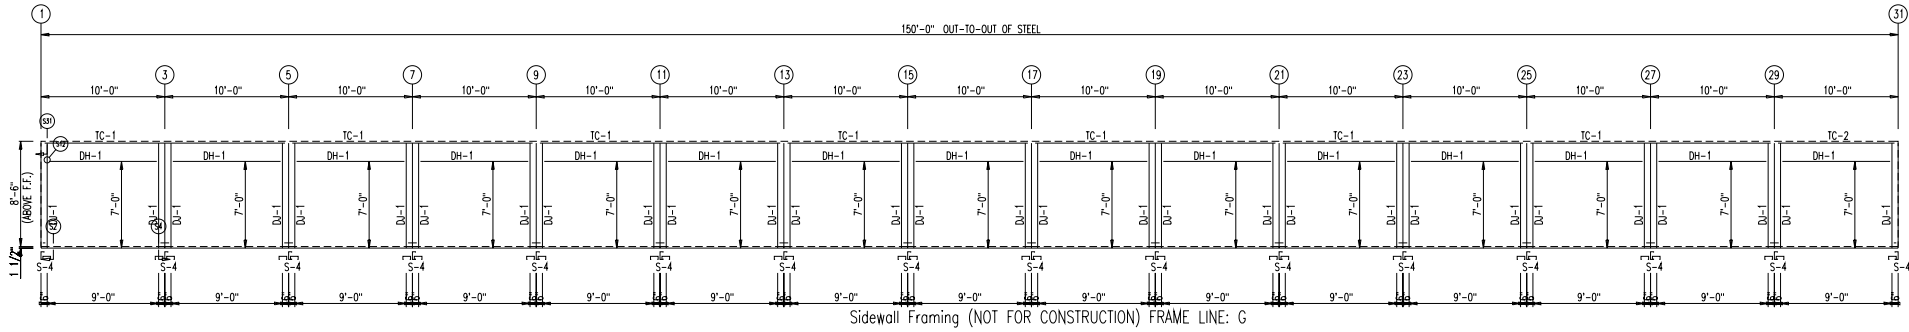

FOR APPROVAL ONLY
NOT FOR CONSTRUCTION

CONFIDENTIAL AND PROPRIETARY INFORMATION
THESE DRAWINGS ARE THE SOLE AND EXCLUSIVE PROPERTY OF THE BUILDING MANUFACTURER. SENSITIVE INFORMATION IS NOT TO BE DISCLOSED OR REPRODUCED IN THESE DRAWINGS MAY ONLY BE USED FOR ITS INTENDED PURPOSE. ANY REUSE OR MISUSE OF THESE DRAWINGS MAY NOT BE USED TO CONSTRUCT THE BUILDING MANUFACTURER THIS DOCUMENT AND ALL COPIES MUST BE RETURNED UPON DEMAND.

PROJECT: **BW625699**ner April 2026
SIZE: 30.0 x 150.0 x 8.5
CITY: Lenoir City
STATE: TN


ROI Metal Buildings
423-991-0130

JOB ID: 94095


Sheet

F2

APPROVAL	PRINTS ISSUED FOR	BY	DATE
			5/6/26

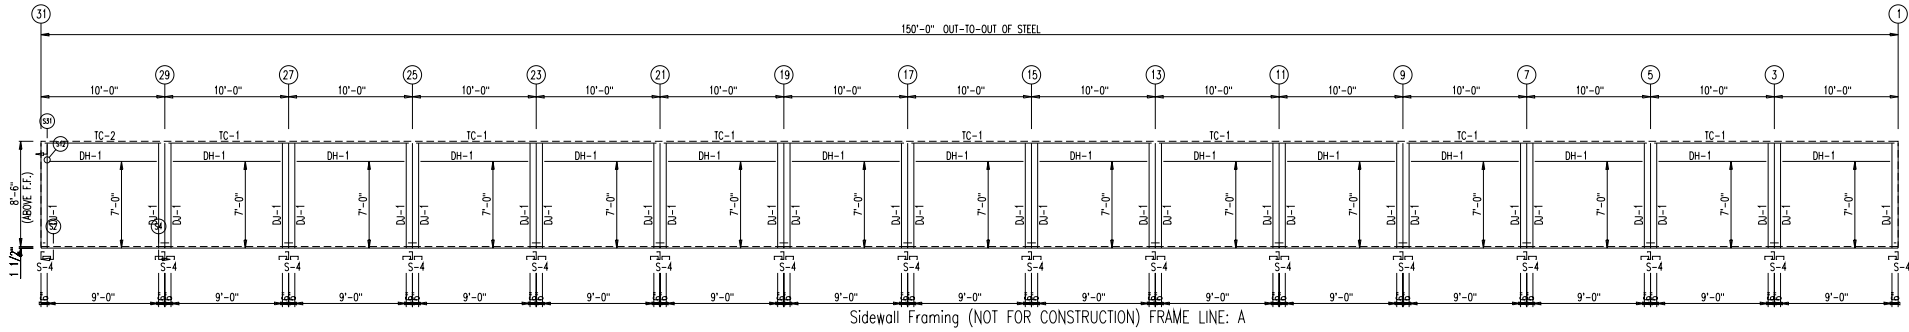

Sidewall Framing (NOT FOR CONSTRUCTION) FRAME LINE: A

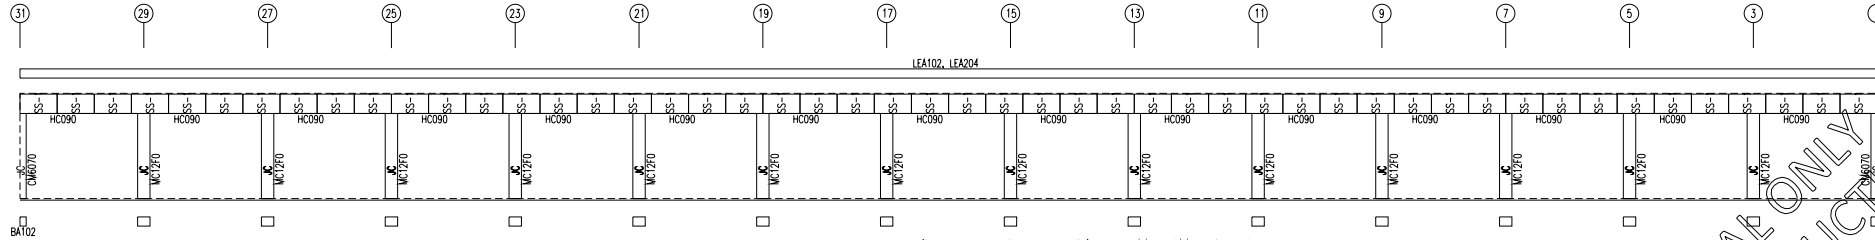

Sidewall Sheeting (NOT FOR CONSTRUCTION) & TRIM FRAME LINE: A
PANELS: 26 Ga. RL - NEED COLOR

FOR APPROVAL ONLY
NOT FOR CONSTRUCTION

CONFIDENTIAL AND PROPRIETARY INFORMATION
THESE DRAWINGS ARE THE SOLE AND EXCLUSIVE PROPERTY OF THE BUILDING MANUFACTURER. SENSITIVE INFORMATION IS NOT TO BE DISCLOSED OR REPRODUCED IN THESE DRAWINGS MAY ONLY BE USED FOR ITS INTENDED PURPOSE. ANY REUSE OR MISUSE OF THESE DRAWINGS MAY NOT BE USED TO CONSTRUCT THE BUILDING MANUFACTURER THIS DOCUMENT AND ALL COPIES MUST BE RETURNED UPON DEMAND.

PROJECT: **FW62809**ner April 2026
SIZE: 30.0 x 150.0 x 8.5
CITY: Lenoir City
STATE: TN


ROI Metal Buildings
423-991-0130

JOB ID: 94095

Sheet

F2

APPROVAL	PRINTS ISSUED FOR	BY	DATE
			5/6/26

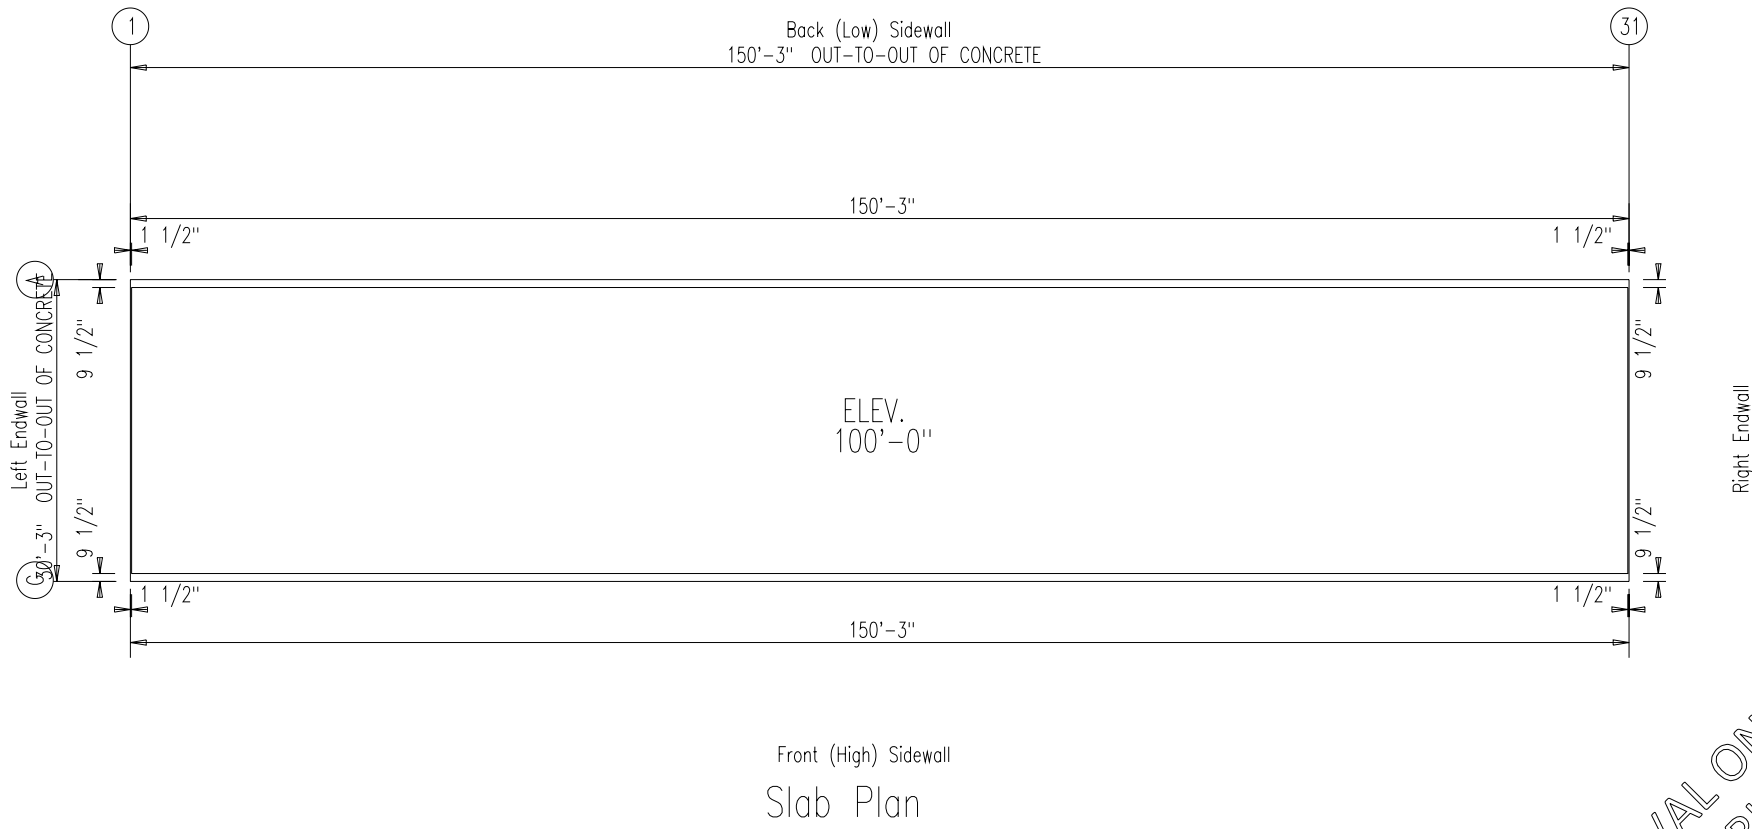

Front (High) Sidewall
Slab Plan

FOR APPROVAL ONLY
NOT FOR CONSTRUCTION

ROI Metal Buildings		PROJECT: BW625699 ner April 2026		CONFIDENTIAL AND PROPRIETARY INFORMATION	
423-991-0130		SIZE: 30.0 x 150.0 x 8.5		THESE DRAWINGS ARE THE SOLE AND EXCLUSIVE PROPERTY OF THE BUILDING MANUFACTURER. SENSITIVE INFORMATION IS NOT TO BE DISCLOSED OR REPRODUCED IN THESE DRAWINGS MAY ONLY BE USED FOR ITS INTENDED PURPOSE. ANY OTHER USE OR REPRODUCTION OF THESE DRAWINGS MAY NOT BE USED TO CONSTRUCT THE BUILDING MANUFACTURER. THIS DOCUMENT AND ALL COPIES MUST BE RETURNED UPON DEMAND.	
JOB ID: 94095		CITY: Lenoir City		APPROVAL	
Sheet		STATE: TN		PRINTS ISSUED FOR	
E4				BY	
				5/6/26	
				DATE	



423-991-0130

SIZE: 30.0 x 150.0 x 8.5

STATE: TN

[illegible]



423-991-0130

SIZE: 30.0 x 150.0 x 8.5

CITY: Lenoir City

STATE: TN

THESE DRAWINGS ARE THE SOLE AND EXCLUSIVE PROPERTY OF THE BUILDING MANUFACTURER. UNLESS OTHERWISE NOTED, ALL INFORMATION CONTAINED HEREIN IS UNCLASSIFIED. INFORMATION CONTAINED IN THESE DRAWINGS MAY ONLY BE USED FOR ITS BENEFIT. THE DISCLOSURE OF THESE DRAWINGS TO UNAUTHORIZED PERSONS IS STRICTLY PROHIBITED. THESE DRAWINGS ARE NOT TO BE REPRODUCED FOR ANY PROJECTS WITHOUT WRITTEN PERMISSION FROM THE BUILDING MANUFACTURER. THIS DOCUMENT AND ALL COPIES MUST BE RETURNED UPON DEMAND.