

STRUCTURAL NOTES

BUILDER / CONTRACTOR IS RESPONSIBLE FOR ENSURING THAT PLANS AND SPECIFICATIONS COMPLY WITH APPLICABLE REQUIREMENTS OF ANY GOVERNING BUILDING AUTHORITY.

METAL BUILDING STRUCTURE DESIGNED PER THE FOLLOWING LOADING:

CODE: IBC, 21
WIND (MPH): 98
EXPOSURE: C
ROOF SNOW LOAD (PSF): 36.12
GROUND SNOW LOAD (PSF): 43
COLLATERAL LOAD (PSF): 0.50
SEISMIC: 0.270
SEISMIC ZONE: D
THERMAL COEFFICIENT: 1.20

DESIGN LOADS DESIGNATED WITHIN CONTRACT AND DRAWINGS DO NOT ALLOW FOR ANY TYPE OF SUSPENDED SYSTEM (E.G. LIGHTS, INSULATION, DUCT WORK, PIPING, ETC.) SUSPENSION OF ANY LOAD INCLUDING SYSTEM IS EXPLICITLY PROHIBITED UNLESS A CORRESPONDING REDUCTION IN CERTIFIED LIVE/SNOW LOADS CAN BE PERMITTED BY CODE.

DESIGN AND SPECIFICATION OF BASE STEEL TO CONCRETE SLAB ANCHORING IS NOT THE RESPONSIBILITY OF THE BUILDING MANUFACTURER.

BUILDING MANUFACTURER ASSUMES NO RESPONSIBILITY FOR CONCRETE SLAB FOUNDATION DESIGN, THICKNESS, MATERIALS, SITE SOIL CONDITIONS OR OTHER CONCRETE/MASONRY CONSTRUCTION.

ALL STRUCTURAL CONNECTIONS ARE TO BE MADE PER FASTENING DETAILS PRESENTED HEREIN. ALL STEEL FRAMING AND SHEETING MATERIALS MUST BE INSTALLED TO VERTICAL PLUMB AND HORIZONTALLY LEVEL.

THE BUILDING MANUFACTURER AND THE PROFESSIONAL ENGINEER SEALING THESE DRAWINGS ARE NOT THE PROFESSIONAL ENGINEER OF RECORD FOR THE ENTIRE PROJECT. THE PROFESSIONAL ENGINEER'S SEAL PERTAINS ONLY TO THE STRUCTURAL DESIGN OF THE METAL BUILDING SYSTEM. IT DOES NOT APPLY TO THE FOUNDATION SYSTEM, MASONRY DESIGN OR ANY OTHER ASPECT OF THE PROJECT UNLESS SPECIFICALLY STATED IN THESE DOCUMENTS.

JOBSITE / FIELD CONDITIONS NOTES:

BUILDING MANUFACTURER ASSUMES NO RESPONSIBILITY FOR ANY LOADS TO STRUCTURE NOT INDICATED AT THE TIME OF PURCHASE. ANY ALTERATIONS TO THE STRUCTURAL SYSTEM, REMOVAL OF ANY COMPONENT PARTS OR THE ADDITION OF OTHER CONSTRUCTION MATERIALS OR LOADS MUST BE DONE UNDER THE DIRECTION OF REGISTERED ARCHITECT, CIVIL OR STRUCTURAL ENGINEER.

ALL CONCRETE AND MASONRY CONSTRUCTION MUST BE FLAT, LEVEL AND SQUARE PER THE SLAB PLAN DIMENSIONS HEREIN.

ALL JOBSITE DIMENSIONS AND CONDITIONS SHALL BE FIELD VERIFIED BEFORE ERECTION OF BUILDING STRUCTURE.

ALL OMISSIONS, CONFLICTS AND DISCREPANCIES SHALL BE REPORTED TO THE BUILDING MANUFACTURER BEFORE PROCEEDING WITH PROJECT WORK.

ALL TEMPORARY SUPPORTS SUCH AS GUYS, BRACES, FALSEWORK, CROWBING, WINDBRACES OR OTHER ELEMENTS REQUIRED FOR THE BUILDING ERECTION ARE TO BE DETERMINED BY AND SUPPLIED BY BUILDER/CONTRACTOR.

BUILDING MANUFACTURER HAS MADE A COMMITMENT TO MANUFACTURE QUALITY BUILDING COMPONENTS THAT CAN BE SAFELY ERECTED, JOB SITE SAFETY INSTRUCTION, SAFETY EQUIPMENT AND CONDITIONS ARE THE RESPONSIBILITY OF THE BUILDER/CONTRACTOR.

ALL COMPONENTS SHIPPED SHALL BE THOROUGHLY INSPECTED AND ACCOUNTED FOR AT THE TIME OF DELIVERY. ALL MATERIAL SHORTAGES OR DEFECTS MUST BE REPORTED WITHIN FIVE (5) WORKING DAYS OF MATERIAL DELIVERY TO THE BUILDING MANUFACTURER.

DAPHRAGM ACTION OF THE METAL PANELS AT INTERIOR PARTITION WALLS IS UTILIZED FOR THE STABILITY OF THIS BUILDING. ANY MODIFICATION OR UNAUTHORIZED CUTTING OF INTERIOR PARTITION PANELS IS EXPRESSLY PROHIBITED BY THE BUILDING MANUFACTURER.

PARTITION PANELS HAVE BEEN SUPPLIED TO REACH ROOF LINE. THE TOP PARTITION PANEL CAN BE NOTCHED TO MATCH ROOF LINE AND CLEAR PURLIN LEG TO CLOSE IN THE UNIT AS DESIRED.

INSTALLATION NOTES:

FIELD CUTTING OF STRUCTURAL, SHEETING AND TRIMS FOR SPLICE AND FINAL FITTING OF COMPONENTS IS REQUIRED.

ALL ROOF PANEL LAPS SHALL BE SEALED WITH 3/8" (MINIMUM) WIDTH MASTIC TAPE AS PROVIDED FOR PROJECT. ALL SHEET PROFILE FOAM CLOSURES AT EAVE, WALL AND RIDGE CONDITIONS AS PROVIDED FOR PROJECT MUST BE INSTALLED AS SHOWN HEREIN.

WALL PANELS AND WALL TRIMS, AT INTERIOR AND EXTERIOR, ARE TO BE SET WITH 1/4" CLEARANCE ABOVE CONCRETE SURFACES AND AT ANY LOCATIONS WHICH MAY BE SUBJECTED TO CONTACT WITH STANDING WATER.

LAP ALL FLASHINGS 2" MINIMUM AND SEAL AS REQUIRED FOR WATER TIGHTNESS

ALLOW 1/4" TOLERANCE AT EACH END FOR PURLINS, HEADERS AND GIRTS.

DRAWING INDEX

A1 LEAD SHEET, GENERAL NOTES, SCHEDULES, ROOF PLAN

A2 ELEVATIONS

A3 ELEVATIONS

A4 ELEVATIONS

A5 SLAB LAYOUT

A6 STUD LAYOUT

A7 UNIT LAYOUT

A8 REACTIONS

STANDARD ABBREVIATIONS

AFB	ABOVE FINISHED FLOOR	FBO	FURNISHED BY OTHERS	OC	ON CENTER
APPROX	APPROXIMATE	FDN	FOUNDATION	OD	OUTSIDE DIAMETER
BLK	BLOCK	FFB	FINISHED FLOOR	OH	OPPOSITE HAND
BLK	BLOCK	FBB	FACE OF BLOCK OR BRICK	OPP	OPPOSITE
BM	BEAM	FTG	FACE OF STEEL	PTN	PARTITION
BTM	BOTTOM	FTT	FEET OR FEET	RAD	RADIUS
BLK	BLOCKING	FOS	FOOTING	REF	REFERENCE
CL	CENTERLINE	GA	GALVANIZED	REQD	REQUIRED
CJ	CAULK JOINT	GALV	GALVANIZED	REINF	REINFORCED
CLD	CEILING	GR	GRADE	ROOF	ROUGH OPENING
COL	COLUMN	GRD	GROUND	SECT	SECTION
CONC	CONCRETE	GR	GRADE	SM	SQUARE FOOTAGE
DET	DETAIL	GRD	GROUND	SQ	SQUARE
DWG	DRAWING	GRD	GROUND	SQ	SQUARE
DM	DIMENSION	GRD	GROUND	SQ	SQUARE
DR	DOOR	GRD	GROUND	SQ	SQUARE
EACH	EACH	GRD	GROUND	SQ	SQUARE
ER	ERECTION TOLERANCE	GRD	GROUND	SQ	SQUARE
EXP	EXPANSION JOINT	GRD	GROUND	SQ	SQUARE
EL	ELEVATION	GRD	GROUND	SQ	SQUARE
EXIST	EXISTING	GRD	GROUND	SQ	SQUARE
EXP	EXPANSION	GRD	GROUND	SQ	SQUARE
EXT	EXTERIOR	GRD	GROUND	SQ	SQUARE
EXT	EXTERIOR INSULATION	GRD	GROUND	SQ	SQUARE
AND FINISH SYSTEM		GRD	GROUND	SQ	SQUARE
EOS	EDGE OF SLAB	GRD	GROUND	SQ	SQUARE

CLOSURE NOTES:

(_) INSIDE CLOSURES INCLUDED FOR LOW EAVE.

INSTALL BTR TAPE ON TOP AND BOTTOM OF INSIDE CLOSURE (SEE DETAILS AND INSTALLATION GUIDE)

(_) INSIDE CLOSURES INCLUDED FOR BASE OF EXTERIOR WALL PANELS.

(_) OUTSIDE CLOSURES INCLUDED FOR RAKE.

(_) OUTSIDE CLOSURES INCLUDED FOR ROOF AND WALL OF HIGH EAVE.

STRUCTURE ABBREVIATIONS

(BA)	- B4216R 4 x 2 x 16GA. ANGLE (5.9)	- FLOOR BASE ANGLE
(BC)	- U42516Z 4 1/8 x 2 7/8 x 16GA. CHANNEL (9.9)	- FLOOR BASE CHANNEL
(FB)	- C4216R 4 x 2 x 16GA. CEE (8.9)	- 4" COLUMN
(CC)	- C62516R 6 x 2 1/2 x 16GA. CEE (11.9)	- 6" COLUMN
(DH)	- C4216R 4 x 2 x 16GA. CEE (8.9)	- DOOR HEAD
(DJ)	- C43516R 4 x 3 1/2 x 16GA. CEE (11.9)	- DOOR JAMB
(RW)	- 26GA. PBR WALL PANEL	- DOOR JAMB
(CL)	- U4216R 4 1/8 x 2 3/8 x 16GA. CHANNEL (8.9)	- EAVE CHANNEL
(ES)	- E64316LR 4 x 6 x 3 x 16GA. STRUT (13.9)	- EAVE STRUT
(FC)	- AS MANUFACTURED	- FLOOR CLIP
(C)	- C4216R 4 x 2 x 16GA. CEE (8.9)	- GIRT
(HA)	- B4216R 4 x 2 x 16GA. ANGLE (5.9)	- HALL TOP ANGLE
(HR)	- C4216R 4 x 2 x 16GA. CEE (8.9)	- DOOR HEAD REINFORCEMENT
(JR)	- C62516R 6 x 2 1/2 x 16GA. CEE (11.9)	- JACK RAPTER
(M)	- C12416R 12 x 4 x 16GA. CEE (20.9)	- MULLION
(MC)	- B4216R 4 x 2 x 16GA. ANGLE (5.9)	- MINI CLIP
(PA)	- C42516R 2 1/2 x 4 x 2 1/2 x 16GA. ZEE (9.9)	- ROOF PURLIN
(P6)	- B62516R 2 1/2 x 6 x 2 1/2 x 16GA. ZEE (11.9)	- ROOF PURLIN
(P8)	- B82516R 2 1/2 x 8 x 2 1/2 x 16GA. ZEE (13.9)	- ROOF PURLIN
(PA)	- B4216R 4 x 2 x 16GA. ANGLE (5.9)	- PARTITION ANGLE
(RA)	- B4216R 4 x 2 x 16GA. ANGLE (5.9)	- RAKE ANGLE
(RS)	- E64316LR 4 x 6 x 3 x 16GA. STRUT (13.9)	- RIDGE STRUT

SHEETING ABBREVIATIONS


(M)	- 29GA. M-LOC WALL PANEL
(RL)	- 29GA. R-LOC WALL PANEL
(PL)	- 29GA. PANEL-LOC WALL PANEL
(RR)	- 26GA. PBR ROOF PANEL
(CL)	- 24GA. CENTRAL-LOC SSR 24" ROOF PANEL
(CL-200)	- SSR LOW FIXED CLIP

FASTENER ABBREVIATIONS

(F1)	- 1/2" x 2 3/4" CONC. EXPANSION ANCHOR	- BASE TO SLAB CONNECTIONS
(F2)	- 12 x 1 1/4" SELF-DRILLING TEK (PLTD)	- STRUCTURAL STEEL CONNECTIONS
(F3)	- 12 x 1 1/4" SELF-DRILLING TEK (PLTD)	- PARTITION SHEETING
(F4)	- 12 x 1 1/4" SELF-DRILLING TEK (PLTD)	- PARTITION ANGLE CONNECTIONS
(F5)	- 12 x 1 1/4" WASHER TEK (PTD)	- EXTERIOR WALL SHEETING
(F6)	- 12 x 1 1/4" WASHER ZAC (PTD)(PLTD)	- ROOF SHEETING
(F7)	- 12 x 1 1/4" WASHER TEK (PTD)	- EXTERIOR TRIM DRILLER
(F8)	- 12 x 7/8" WASHER TEK (PTD)	- EXTERIOR WALL PANEL LAP
(F9)	- 12 x 7/8" WASHER ZAC (PTD)(PLTD)	- ROOF PANEL LAP
(F10)	- 12 x 7/8" WASHER TEK (PTD)	- EXTERIOR TRIM LAP
(F11)	- 1/8" POP RIVET	- EXTERIOR TRIM
(F12)	- 12 x 1 1/4" WASHER TEK (PTD)	- INTERIOR WALL SHEETING
(F13)	- 12 x 1 1/4" WASHER TEK (PTD)	- INTERIOR TRIM DRILLER
(F14)	- 12 x 7/8" WASHER TEK (PTD)	- INTERIOR WALL PANEL LAP
(F15)	- 12 x 7/8" WASHER TEK (PTD)(PLTD)	- INTERIOR TRIM LAP
(F17)	- 1/4"-14 x 1" SDS W/ WASHER #1(PLTD)	- "CL" CLIP/STRUCTURE CONNECTIONS
(F18)	- 1/4"-14 x 1 1/4" SDS ZAC W/WASHER #1(PTD)(PLTD)	- "CL" ROOF DRILLER
(F19)	- 14 x 7/8" SDS ZAC W/ WASHER #4(PTD)(PLTD)	- "CL" ROOF LAP
(F20)	- 1/4"-14 x 1 1/4" SDS ZAC W/WASHER #1(PTD)(PLTD)	- "CL" TRIM DRILLER
(F21)	- 14 x 7/8" SDS ZAC W/WASHER #4(PTD)(PLTD)	- "CL" TRIM LAP

TRIM ABBREVIATIONS

(BTR)	- 7/8" ROLL MASTIC	(ICB)	- INSIDE CORNER BOX
(CLIN)	- R PANEL INSIDE FOAM CLOSURE	(JA)	- DOOR JAMB TRIM
(CLOUT)	- R PANEL OUTSIDE FOAM CLOSURE	(JC)	- DOOR JAMB COVER TRIM
(GECEEL)	- GUTTER SEAL	(MC)	- DOOR MULLION COVER TRIM
(IN)	- R PANEL INSIDE CORNER TRIM	(OCB)	- OUTSIDE CORNER BOX
(OU)	- R PANEL OUTSIDE CORNER TRIM	(PB)	- PEAK BOX
(CM)	- DOOR CORNER MULLION TRIM	(REND)	- RAKE TRIM END CAP
(DK)	- DOWNSPOUT WITH KICK OUT	(RT)	- RAKE TRIM
(DSS)	- DOWNSPOUT STRAP	(TI)	- ROOF TIE IN TRIM
(EF)	- EAVE FLASHING	(TRP)	- ROOF STEP TRANSITION FLASHING
(FCE)	- FORMED RIDGE CAP	(4SP)	- 40Z TOUCH UP SPRAY PAINT
(GC)	- GUTTER END CAP		
(GS)	- GUTTER HANGER STRAP		
(GU)	- GUTTER		
(HC)	- DOOR HEAD COVER TRIM		
(HE)	- DOOR HEAD TRIM		
(HT)	- HALL TOP TRIM		

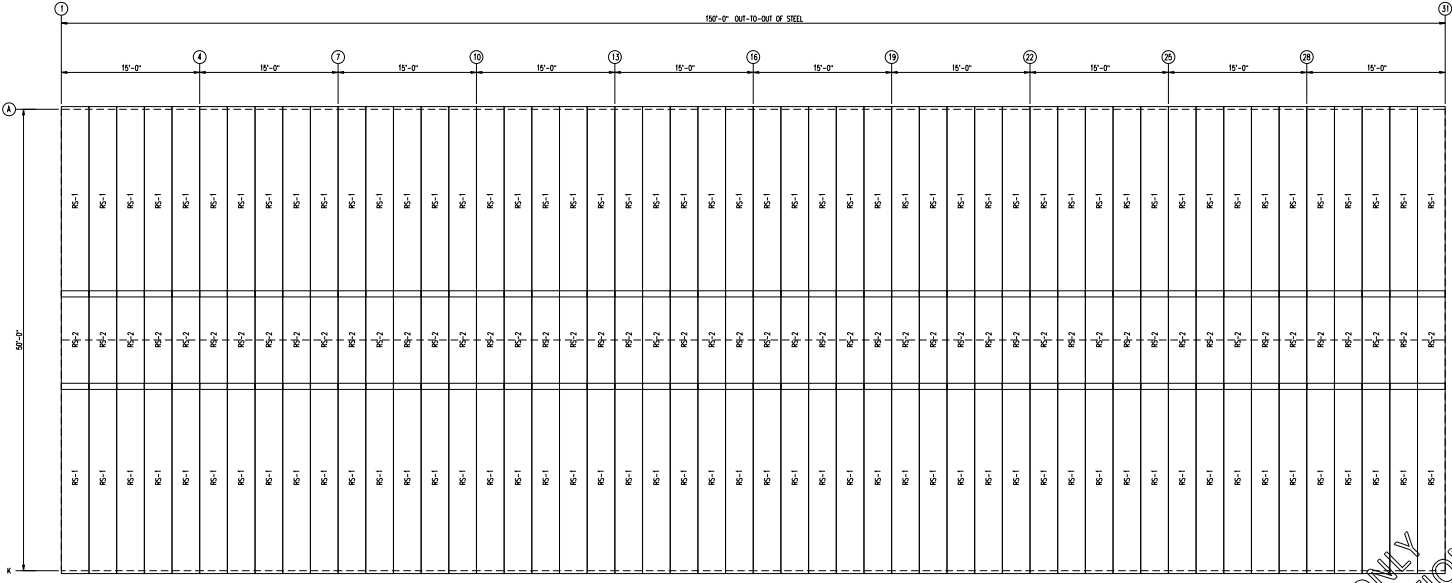

KEY PLAN
not to scale

ROI Metal Buildings

423-991-0130

Sheet

F1

PROJECT: B00025100916 Special

SIZE: 50.0 x 150.0 x 16.0

CITY: Lenoir City

STATE: TN

CONFIDENTIAL AND PROPRIETARY INFORMATION

THESE DRAWINGS ARE THE SOLE AND EXCLUSIVE PROPERTY OF THE BUILDING MANUFACTURER. SENSITIVE INFORMATION IS CONTAINED HEREIN. NO PART OF THESE DRAWINGS MAY BE USED FOR ANY PROJECT WITHOUT THE WRITTEN PERMISSION OF THE BUILDING MANUFACTURER. UNAUTHORIZED REPRODUCTION OF THESE DRAWINGS MAY NOT BE USED TO CONSTRUCT THE BUILDING. BUILDING MANUFACTURER, THIS DOCUMENT AND ALL COPIES MUST BE RETURNED UPON DEMAND.


APPROVAL

PRINTS ISSUED FOR


BY

DATE


4/24/26

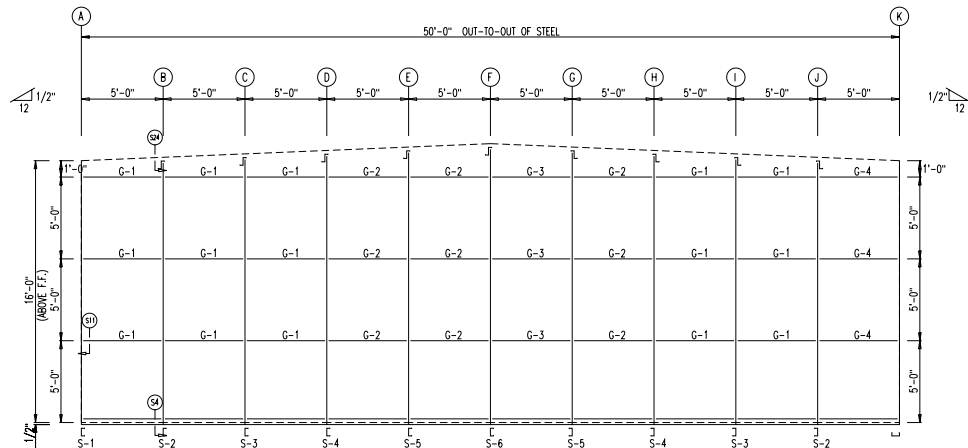


ENDWALL FRAMING FRAME LINE: 1

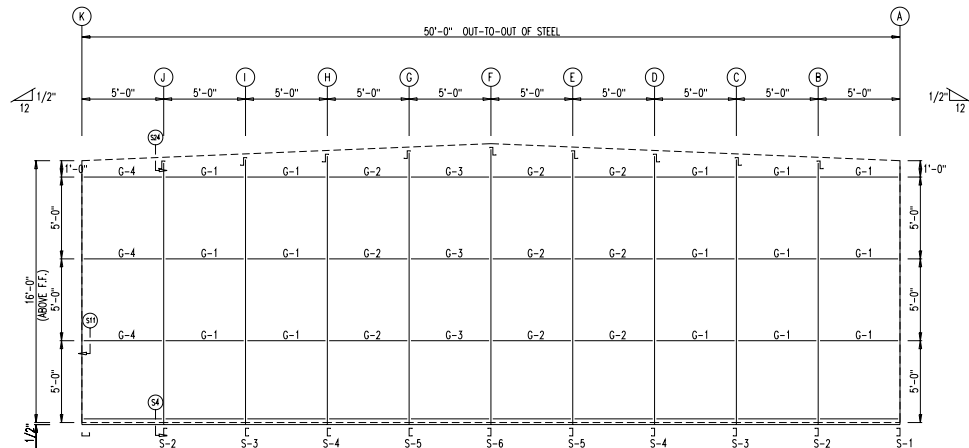

ENDWALL FRAMING FRAME LINE: 31

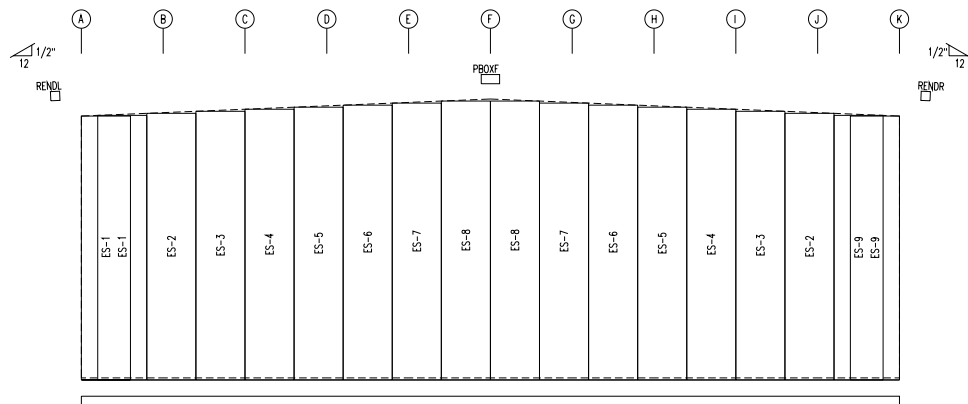

ENDWALL SHEETING & TRIM FRAME LINE: 1
PANELS: 26 Ga. RL - NEED COLOR

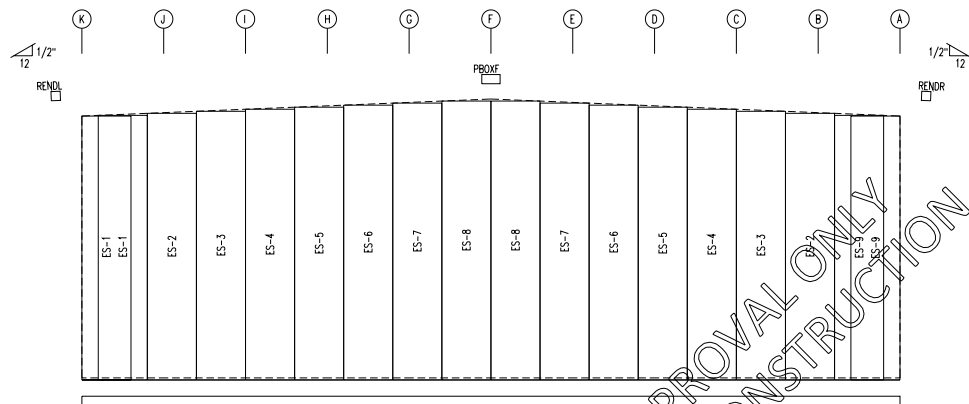

ENDWALL SHEETING & TRIM FRAME LINE: 31
PANELS: 26 Ga. RL - NEED COLOR

FOR APPROVAL ONLY
NOT FOR CONSTRUCTION

APPROVAL	PRINTS ISSUED FOR	BY	DATE
			4/24/26

CONFIDENTIAL AND PROPRIETARY INFORMATION
THESE DRAWINGS ARE THE SOLE AND EXCLUSIVE PROPERTY OF THE BUILDING MANUFACTURER. NO PART OF THESE DRAWINGS MAY BE REPRODUCED OR TRANSMITTED IN ANY FORM OR BY ANY MEANS, ELECTRONIC OR MECHANICAL, WITHOUT THE WRITTEN PERMISSION OF THE BUILDING MANUFACTURER. THESE DRAWINGS MAY NOT BE USED TO CONSTRUCT THE BUILDING MANUFACTURER'S PRODUCT AND ALL COPIES MUST BE RETURNED UPON DEMAND.


PROJECT: B00021500916 Special
SIZE: 50.0 x 150.0 x 16.0
CITY: Lenoir City
STATE: TN

ROI Metal Buildings
423-991-0130

JOB ID: 94493

Sheet

F2

 

FOR APPROVAL ONLY
NOT FOR CONSTRUCTION

ROI Metal Buildings 423-991-0130

JOB ID: 94493

Sheet


E2

PROJECT: 500(251009)6 Special
SIZE: 50.0 x 150.0 x 16.0
CITY: Lenoir City
STATE: TN


CONFIDENTIAL AND PROPRIETARY INFORMATION

THESE DRAWINGS ARE THE SOLE AND EXCLUSIVE PROPERTY OF THE BUILDING MANUFACTURER. NO PART OF THESE DRAWINGS MAY BE REPRODUCED, COPIED, OR TRANSMITTED IN ANY FORM OR BY ANY MEANS, ELECTRONIC OR MECHANICAL, INCLUDING PHOTOCOPYING, RECORDING, OR BY ANY INFORMATION STORAGE AND RETRIEVAL SYSTEM, WITHOUT THE WRITTEN PERMISSION OF THE BUILDING MANUFACTURER. THESE DRAWINGS MAY ONLY BE USED FOR ITS BENEFIT. THE DISCLOSURE OF THESE DRAWINGS TO UNAUTHORIZED PERSONS IS STRICTLY PROHIBITED. THESE DRAWINGS MAY NOT BE USED TO CONSTRUCT LIKE OR SIMILAR BUILDINGS WITHOUT THE WRITTEN PERMISSION OF THE BUILDING MANUFACTURER. THIS DOCUMENT AND ALL COPIES MUST BE RETURNED UPON DEMAND.

[illegible]

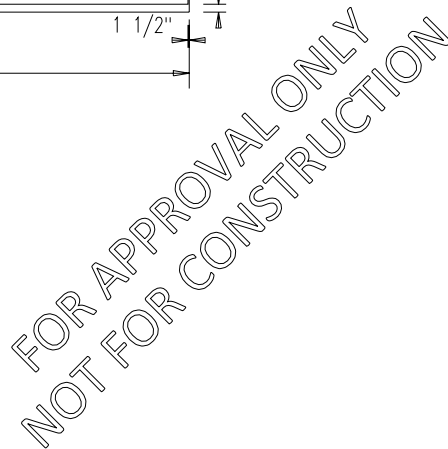

ROI Metal Buildings	PROJECT: BW0251009 6 Special	CONFIDENTIAL AND PROPRIETARY INFORMATION
JOB ID: 94493	SIZE: 50.0 x 150.0 x 16.0	THESE DRAWINGS ARE THE SOLE AND EXCLUSIVE PROPERTY OF THE COMPANY. ALL RIGHTS ARE RESERVED. NO PART OF THESE DRAWINGS MAY BE REPRODUCED OR TRANSMITTED IN ANY FORM OR BY ANY MEANS, ELECTRONIC OR MECHANICAL, WITHOUT THE WRITTEN PERMISSION OF THE COMPANY. THE COMPANY ASSUMES NO LIABILITY FOR ANY ERRORS OR OMISSIONS. THE USER AGREES TO HOLD THE COMPANY HARMLESS FROM ANY AND ALL CLAIMS, DAMAGES, LOSSES, AND EXPENSES, INCLUDING ATTORNEY'S FEES, ARISING OUT OF OR RESULTING FROM THE USE OF THESE DRAWINGS. COPIES MUST BE RETURNED UPON DEMAND.
Sheet	CITY: Lenoir City	
E4	STATE: TN	
		APPROVAL
		PRINTS ISSUED FOR
		BY
		DATE

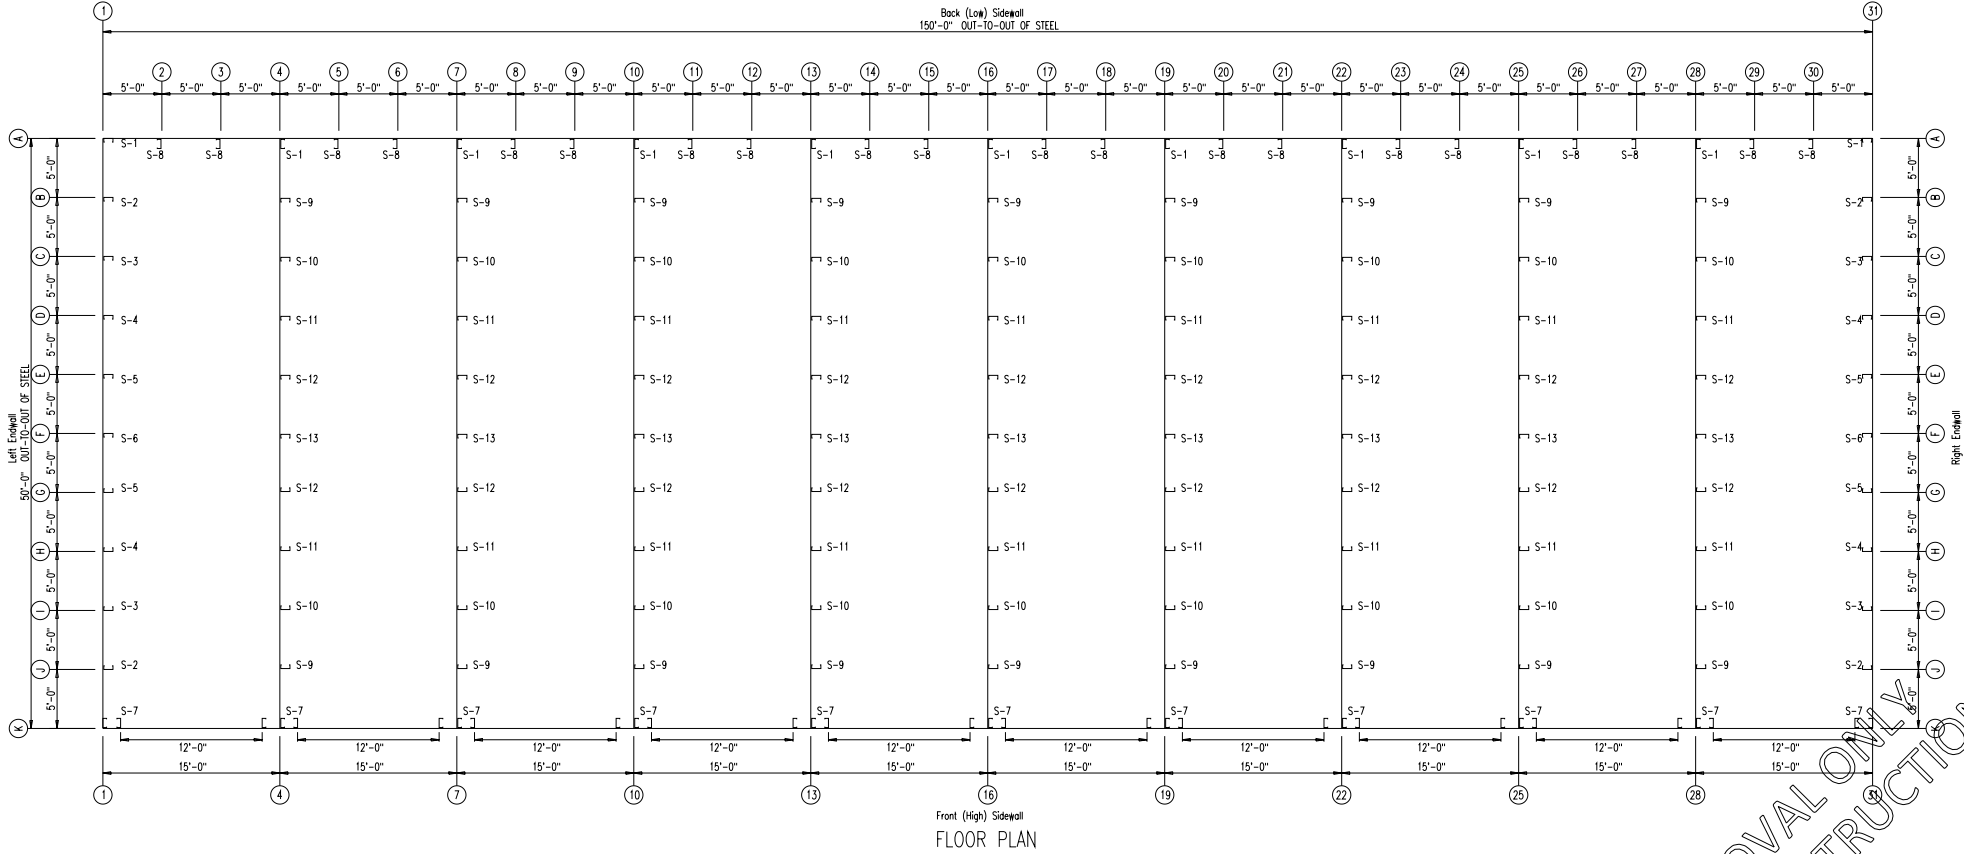

FOR APPROVAL ONLY
NOT FOR CONSTRUCTION

CONFIDENTIAL AND PROPRIETARY INFORMATION
THESE DRAWINGS ARE THE SOLE AND EXCLUSIVE PROPERTY OF THE BUILDING MANUFACTURER. NO PART OF THESE DRAWINGS MAY BE USED FOR ANY OTHER PROJECT WITHOUT THE WRITTEN PERMISSION OF THE BUILDING MANUFACTURER. UNAUTHORIZED PERSONS ARE STRICTLY PROHIBITED FROM REPRODUCING OR USING THESE DRAWINGS FOR ANY PURPOSE. THE BUILDING MANUFACTURER SHALL NOT BE USED TO CONSTRUCT THE BUILDING. 

PROJECT: 500(215009)6 Special
SIZE: 50.0 x 150.0 x 16.0
CITY: Lenoir City
STATE: TN


ROI Metal Buildings
423-991-0130

JOB ID: 94493

Sheet

F5

APPROVAL	PRINTS ISSUED FOR	BY	DATE
			4/24/26

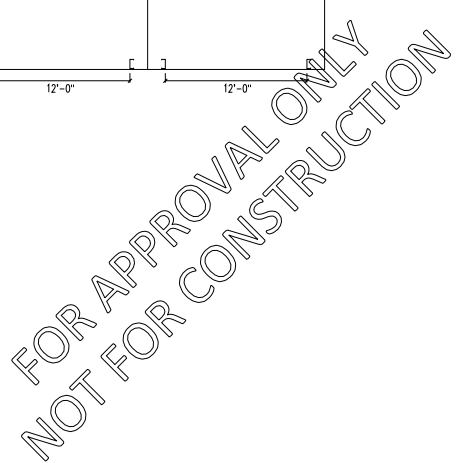

ROI Metal Buildings
423-991-0130

E6

STATE: TN

[illegible]