

STRUCTURAL NOTES

BUILDER / CONTRACTOR IS RESPONSIBLE FOR ENSURING THAT PLANS AND SPECIFICATIONS COMPLY WITH APPLICABLE REQUIREMENTS OF ANY GOVERNING BUILDING AUTHORITY.

METAL BUILDING STRUCTURE DESIGNED PER THE FOLLOWING LOADING:

CODE:IBC 211
WIND (MPH):115
EXPOSURE: C
ROOF SNOW LOAD (PSF):29.40
GROUND SNOW LOAD (PSF): 35
COLLATERAL LOAD (PSF)0.50
SEISMIC: 0.270
SEISMIC ZONE:D
THERMAL COEFFICIENT: 1.20

DESIGN LOADS DESIGNATED WITHIN CONTRACT AND DRAWINGS DO NOT ALLOW FOR ANY TYPE OF SUPERSTRESS, SUSTAINED, SHOCKS, INSULATION, DUCT WORK, PIPING, ETC.) SUSPENSION OF ANY LOAD INDUCING SYSTEM IS EXPLICITLY PROHIBITED UNLESS A CORRESPONDING REDUCTION IN CERTIFIED LIVE/SNOW LOADS CAN BE PERMITTED BY CODE.

DESIGN AND SPECIFICATION OF BASE STEEL TO CONCRETE SLAB ANCHORING IS NOT THE RESPONSIBILITY OF THE BUILDING MANUFACTURER.

BUILDING MANUFACTURER ASSUMES NO RESPONSIBILITY FOR CONCRETE SLAB FOUNDATION DESIGN, THICKNESS, MATERIALS, SITE SOIL CONDITIONS OR OTHER CONCRETE/MASONRY CONSTRUCTION.

ALL STRUCTURAL CONNECTIONS ARE TO BE MADE PER FASTENING DETAILS PRESENTED HEREIN. ALL STEEL FRAMING AND SHEETING MATERIALS MUST BE INSTALLED TO VERTICAL PLUMB AND HORIZONTALLY LEVEL.

THE BUILDING MANUFACTURER AND THE PROFESSIONAL ENGINEER SEALING THESE DRAWINGS ARE NOT THE PROFESSIONAL ENGINEER OF RECORD FOR THE ENTIRE PROJECT. THE PROFESSIONAL ENGINEER'S SEAL PERTAINS ONLY TO THE STRUCTURAL DESIGN OF THE METAL BUILDING SYSTEM. IT DOES NOT APPLY TO DESIGN SYSTEMS, MASONRY DESIGN OR ANY OTHER ASPECT OF THE PROJECT UNLESS SPECIFICALLY STATED IN THESE DOCUMENTS.

BUILDING MANUFACTURER ASSUMES NO RESPONSIBILITY FOR ANY LOADS TO STRUCTURE NOT INDICATED AT THE TIME OF PURCHASE. ANY ALTERATIONS TO THE STRUCTURAL SYSTEM, REMOVAL OF ANY MATERIALS, OR ADDITION OF ANY MATERIALS, OR ADDITION OF ANY MATERIALS OR LOADS MUST BE DONE UNDER THE DIRECTION OF REGISTERED ARCHITECT, CIVIL OR STRUCTURAL ENGINEER.

ALL CONCRETE AND MASONRY CONSTRUCTION MUST BE FLAT, LEVEL AND SQUARE PER THE SLAB PLAN DIMENSIONS HEREIN.

ALL JOIST DIMENSIONS AND CONDITIONS SHALL BE FIELD VERIFIED BEFORE ERECTION OF BUILDING STRUCTURE.

ALL OMISSIONS, CONFLICTS AND DISCREPANCIES SHALL BE REPORTED TO THE BUILDING MANUFACTURER BEFORE PROCEEDING WITH PROJECT WORK/CONTRACT.

ALL TEMPORARY SUPPORTS SUCH AS GUYS, BRACES, FALSWORK, CRIBBING, WINGBRACES OR OTHER ELEMENTS REQUIRED FOR THE BUILDING ERECTION ARE TO BE DETERMINED BY AND SUPPLIED BY BUILDER/CONTRACTOR.

BUILDING MANUFACTURER HAS MADE A COMMITMENT TO MANUFACTURE QUALITY BUILDING COMPONENTS THAT CAN BE SAFELY ERECTED, JOB SITE SAFETY INSTRUCTION, SAFETY EQUIPMENT AND CONDITIONS ARE THE RESPONSIBILITY OF THE BUILDER/CONTRACTOR.

ALL COMPONENTS SHIPPED SHALL BE THOROUGHLY INSPECTED AND ACCOUNTED FOR AT THE TIME OF DELIVERY. ALL MATERIAL SHORTAGES OR DEFECTS MUST BE REPORTED WITHIN FIVE (5) WORKING DAYS OF MATERIAL DELIVERY TO THE BUILDING MANUFACTURER.

DIAPHRAGM ACTION OF THE METAL PANELS AT INTERIOR PARTITION WALLS IS UTILIZED FOR THE STABILITY OF THIS BUILDING. ANY MODIFICATION OR UNAUTHORIZED CUTTING OF INTERIOR PARTITION IS EXPRESSLY PROHIBITED BY THE BUILDING MANUFACTURER.

PARTITION PANELS HAVE BEEN SUPPLIED TO REACH ROOF LINE. THE TOP PARTITION PANEL CAN BE NOTCHED TO MATCH ROOF LINE AND CLEAR PURLIN LEG TO CLOSE IN THE UNIT AS DESIRED.

FIELD CUTTING OF STRUCTURAL, SHEETING AND TRIMS FOR SPACE AND FINAL FITTING OF COMPONENTS IS REQUIRED.

ALL ROOF PANEL LAPS SHALL BE SEALED WITH 3/8" (MINIMUM) WIDTH MASTIC TAPE AS PROVIDED FOR PROJECT. ALL SHEET PROFILE FOAM CLOSURES AT EAVE, WALL AND RIDGE CONDITIONS ARE PROVIDED FOR PROJECT MUST BE INSTALLED AS SHOWN HEREIN.

WALL PANELS AND WALL TRIMS, AT INTERIOR AND EXTERIOR, ARE TO BE SET WITH 1/4" CLEARANCE ABOVE CONCRETE SURFACES AND AT ANY LOCATIONS WHICH MAY BE SUBJECTED TO CONTACT WITH STANDING WATER.

ALL LAP FLASHINGS 2" MINIMUM AND SEAL AS REQUIRED FOR WATER TIGHTNESS

ALLOW 1/4" TOLERANCE AT EACH END FOR PURLINS, HEADERS AND GIRTS.

[illegible]

AFB	ABOVE FINISHED FLOOR	FBO	FURNISHED BY OTHERS	OC	ON CENTER
APP APPROX	APPROXIMATE	FBD FOUNDATION		OD	OUTSIDE DIAMETER
BK BLOCK	BUILDING	FBL FINISHED FLOOR		OH	OPPOSITE HAND
BLK BLOCK		FBS FACE OF BLOCK OR BRICK		OP	OPPOSITE
BN BEAM		FBS FACE OF SLAB		PTN PARTITION	
BOB BOTTOM		FBS FOOT OF FEET		RADII	
BOB BLOCKING		FTG FOOTING		REF REFERENCE	
CBJ CEMENT		GAU GAUGE		REQ REQUIRED	
CLJ CALK CUT		GLV GALVANIZED		REIN REINFORCED	
CLG CONC		GC GENERAL CONTRACTOR		RO ROUGH OPENING	
CLM COLUMN		GR GRADE		SC SECTION	
CONC CONC		GW GROUND WATER		SQ SQUARE	
CS CEMENT		HW HORIZONTAL WALL BOARD		SW SW	
DBL DOUBLE		HZ HORIZONTAL		SQ SQUARE	
DET DETAIL		HT HEIGHT		STD STANDARD	
DIAM DIAMETER		INS INSIDE DIAMETER		STEE STEEL	
DWG DRAWING		INS INSULATION		TOS TOP OF BEAM	
DWG DIMENSION		INT INTERIOR		TOS TOP OF CONCRETE	
DR DR		INFO INFORMATION		TOS TOP OF CONCRETE	
EJ EACH		JT JOINT		TOW TOP OF WALL	
EJ EJECTION TOLERANCE		MAX MAXIMUM		TUB TUBES	
EX EXPANSION JOINT		MIN MINIMUM		TYP TYPICAL	
EXT EXTENSION		MT MISCELLANEOUS		UND UNDER	
EXIST EXISTING		MTC METAL		VAR VARIOUS	
EXP EXPANSION		NIC NOT IN CONTRACT		VERT VERTICAL	
EXT EXTENSION		NSC NOT TO SCALE		WF WELDED IN FIELD	
EXIS EXISTING INSULATION		NA NOT APPLICABLE		WO WITHOUT	
EXIS EXISTING INSULATION		NUM NUMBER		WT WEIGHT	
EOS EDGE OF SLAB		OA OVERALL			

ROOF SHEETING & TRIM
PANELS: 26 Ga. RL - Colvolute Plus

CLOSURE NOTE:
 () INSIDE CLOSURES INCLUDED FOR LOW EAVE.
 INSTALL BTR TAPE ON TOP AND BOTTOM OF INSIDE
 CLOSURE (SEE DETAILS AND INSTALLATION GUIDE)
 () INSIDE CLOSURES INCLUDED FOR BASE OF
 EXTERIOR WALL PANELS.
 () OUTSIDE CLOSURES INCLUDED FOR RAKE.
 () OUTSIDE CLOSURES INCLUDED FOR ROOF
 AND WALL OF HIGH EAVE.

(BA)	- B4216R 4 X 2 X 16GA. ANGLE (5.9)	- FLOOR BASE ANGLE
(BB)	- U24516Z 1/4 X 1/8 X 7/16 X 16GA. CHANNEL (9.9)	- FLOOR BASE CHANNEL
(CB)	- C4216R 4 X 2 X 16GA. ANGLE (8.9)	- 4" COLUMN
(CC)	- C62516R 6 X 2 1/2 X 16GA. CEE (11.9)	- 6" COLUMN
(DC)	- D4216R 4 X 2 X 16GA. CEE (8.9)	- DOOR HEAD
(DD)	- C43516R 4 X 1 X 16GA. ANGLE (11.9)	- DOOR HEAD ANGLE
(EH)	- U4216R 1/4 X 1/8 X 2 5/8 X 16GA. CHANNEL (8.9)	- EAVE CHANNEL
(ES)	- E64316LR 4 X 6 X 3 X 16GA. STRUT (13.9)	- EAVE STRUT
(FC)	- AS MANUFACTURED	- FLOOR CLIP
(G)	- C4216R 4 X 2 X 16GA. CEE (8.9)	- GIRT
(HA)	- B4216R 4 X 2 X 16GA. ANGLE (5.9)	- HALL TOP ANGLE
(HB)	- C4216R 4 X 2 X 16GA. ANGLE (8.9)	- HALL HEAD REINFORCEMENT
(JR)	- C62516R 6 X 2 1/2 X 16GA. CEE (11.9)	- JACK Rafter
(M)	- L12416R 12 X 4 X 16GA. CEE (20.9)	- MULLION
(MC)	- B4216R 4 X 2 X 2" LONG 16GA. ANGLE (5.9)	- MINE CLIP
(PA)	- Z42516R 2 1/2 X 2 X 1/2 X 16GA. ZEE (9.9)	- PURR PURLIN
(PB)	- Z62516R 2 1/2 X 6 X 1/2 X 16GA. ZEE (11.9)	- PURR PURLIN
(PC)	- Z62516R 2 1/2 X 6 X 1/2 X 16GA. ZEE (15.9)	- PURR PURLIN
(PA)	- B4216R 4 X 2 X 16GA. ANGLE (5.9)	- PARTITION ANGLE
(RB)	- B4216R 4 X 2 X 16GA. ANGLE (5.9)	- RAKE ANGLE
(RS)	- E64316LR 4 X 6 X 3 X 16GA. STRUT (13.9)	- RIDGE STRUT

(NL) - 29CA. N-LOC WALL PANEL
(RL) - 29CA. R-LOC WALL PANEL
(PL) - 29CA. PANEL-LOC WALL PANEL
(RR) - 26CA. PBR ROOF PANEL
(RW) - 26CA. PBR WALL PANEL
(CL) - 24CA. CENTRAL-LOC SSR
24" ROOF PANEL
(CL-200) - SSR LOW FIXED CLIP

(71) - 1/2" x 2 3/4" CONC. EXPANSION ANCHOR	- BASE TO SLAB CONNECTIONS
(72) - 12 x 1 SELF-DRILLING TEK (PLTD)	- STRUCTURAL STEEL CONNECTIONS
(73) - 12 x 1 SELF-DRILLING TEK (PLTD)	- PARTITION SHEETING
(74) - 12 x 2 SELF-DRILLING TEK (PLTD)	- PARTITION ANGLE CONNECTIONS
(75) - 12 x 1 1/4 WASHER TEK (PTD)	- EXTERIOR WALL SHEETING
(76) - 12 x 1 1/4 WASHER ZAC (PTD)(PLTD)	- ROOF SHEETING
(77) - 12 x 1 1/4 WASHER TEK (PTD)	- EXTERIOR TRIM DRILLER
(78) - 12 x 7/8 WASHER TEK (PTD)	- EXTERIOR WALL PANEL LAP
(79) - 12 x 7/8 WASHER TEK (PTD)(PLTD)	- EXTERIOR PANEL LAP
(80) - 12 x 7/8 WASHER TEK (PTD)	- EXTERIOR TRIM LAP
(81) - 1/8 POP RIVET	- EXTERIOR TRIM
(82) - 12 x 1 1/4 WASHER TEK (PTD)	- INTERIOR WALL SHEETING
(83) - 12 x 1 1/4 WASHER TEK (PTD)	- INTERIOR TRIM DRILLER
(84) - 12 x 7/8 WASHER TEK (PTD)	- INTERIOR WALL PANEL LAP
(85) - 12 x 7/8 WASHER TEK (PTD)(PLTD)	- INTERIOR TRIM LAP
(86) - 1/4 - 1/4 x 1 1/4 SDS W/ WASHER (PLTD) "CL" CLIP/STRUCTURE CONNECTIONS	
(87) - 1/4 - 1/4 x 1 1/4 SDS W/ WASHER (PLTD)(PTD) "CL" TRIM DRILLER	
(88) - 1/4 - 1/4 x 1 1/4 SDS W/ WASHER (PLTD)(PTD) "CL" ROOF LAP	
(89) - 1/4 - 1/4 x 1 1/4 SDS W/ WASHER (PLTD)(PTD) "CL" TRIM DRILLER	
(90) - 1/4 - 1/4 x 1 1/4 SDS W/ WASHER (PLTD)(PTD) "CL" TRIM LAP	

(BTR)	- 7/8" ROLL MASTIC	(ICB)	- INSIDE CORNER BOX
(CLN)	- R PANEL INSIDE FOAM CLOSURE	(JAL)	- DOOR JAMB TRIM
(CLOUT)	- R PANEL OUTSIDE FOAM CLOSURE	(JC)	- DOOR JAMB COVER TRIM
(GECEL)	- GUTTER SEAL	(MC)	- DOOR MULLION COVER TRIM
(N)	- R PANEL INSIDE CORNER TRIM	(OCB)	- OUTSIDE CORNER BOX
(OU)	- R PANEL OUTSIDE CORNER TRIM	(PB)	- PEAK BOX
(CM)	- DOOR CORNER MULLION TRIM	(REND)	- RAKE TRIM END CAP
(DK)	- DOWNSPOUT WITH KICK OUT	(RT)	- RAKE TRIM
(DSS)	- DOWNSPOUT STRAP	(TI)	- ROOF TIE IN TRIM
(EF)	- EAVE FLASHING	(TR)	- ROOF STEP TRANSITION FLASHING
(FRC)	- FORMED RIDGE CAP	(4SP)	- 40Z TOUCH UP SPRAY PAINT
(GE)	- GUTTER END CAP		
(GS)	- GUTTER HANGER STRAP		
(GU)	- GUTTER		
(HC)	- DOOR HEAD COVER TRIM		
(HE)	- DOOR HEAD TRIM		
(HE)	- HIGH EAVE TRIM		
(HT)	- HALL TOP TRIM		

FOR APPROVAL ONLY
NOT FOR CONSTRUCTION

ERECTOR NOTE:
A DETAILED INSTALLATION GUIDE IS AVAILABLE AND SHOULD BE
CONSULTED DURING THE ERECTION OF THIS BUILDING PACKAGE.
PLEASE CONTACT US IF YOU HAVE NOT RECEIVED A COPY OF
THE INSTALLATION GUIDE AND ONE WILL BE PROVIDED TO YOU.

THESE DRAWINGS ARE THE SOLE AND EXCLUSIVE PROPERTY OF THE BUILDING MANUFACTURER, CONFIDENTIAL, AND PROPRIETARY INFORMATION. UNLESS OTHERWISE INDICATED, THESE DRAWINGS ARE NOT TO BE REPRODUCED, COPIED, OR TRANSMITTED IN ANY FORM OR BY ANY MEANS, ELECTRONIC OR MECHANICAL, INCLUDING PHOTOCOPYING, RECORDING, OR BY ANY INFORMATION STORAGE AND RETRIEVAL SYSTEM, WITHOUT WRITTEN PERMISSION FROM THE BUILDING MANUFACTURER. THIS DOCUMENT AND ALL COPIES MUST BE RETURNED UPON DEMAND.

PROJECT: BW62 Bridge	April 2026
SIZE: 40.0 x 100.0	x 8.5
CITY: Lenoir	City
STATE: TN	



ROI Metal Buildings
423-991-0130

JOB ID: 94097

Sheet

E1

APPROVAL	6/12/26
PRINTS ISSUED FOR	DATE
BY	

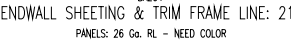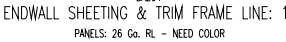

ES-6	ES-5	ES-4	ES-3	ES-2	ES-1
------	------	------	------	------	------


FRAME LINE: 21
D COLOR



THESE DRAWINGS ARE THE SOLE AND EXCLUSIVE PROPERTY OF THE BUILDING MANUFACTURER, SENSITIVE, PRIVILEGED, AND CONFIDENTIAL INFORMATION CONTAINED IN THESE DRAWINGS MAY ONLY BE USED FOR ITS INTENDED PURPOSE. ANY REPRODUCTION OR DISTRIBUTION OF THESE DRAWINGS TO ANY OTHER PERSONS WITHOUT THE EXPRESS WRITTEN PERMISSION OF THE BUILDING MANUFACTURER IS STRICTLY PROHIBITED. UNAUTHORIZED PERSONS ARE STRICTLY PROHIBITED FROM THESE DRAWINGS MAY NOT BE USED TO CONSTRUCT LIKE PROJECTS WITHOUT WRITTEN PERMISSION FROM THE BUILDING MANUFACTURER. THIS DOCUMENT AND ALL COPIES MUST BE RETURNED UPON DEMAND.

PROJECT: BW625000	April 2026
SIZE:	40.0 x 100.0 x 8.5
CITY:	Lenoir City
STATE:	TN

ROI Metal Buildings
423-991-0130
JOB ID: 94097
Sheet
E2

[illegible]

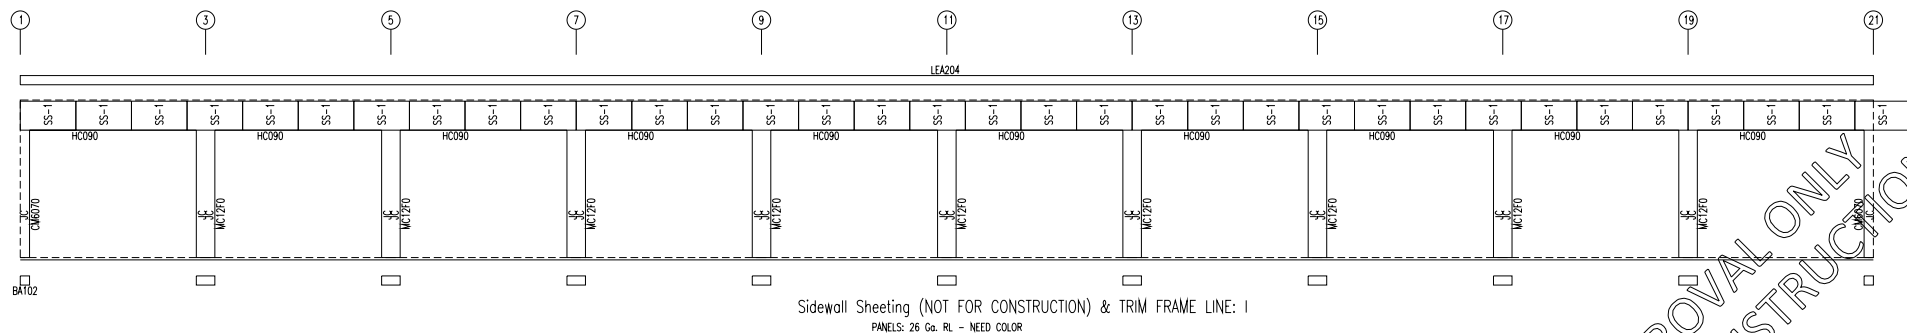


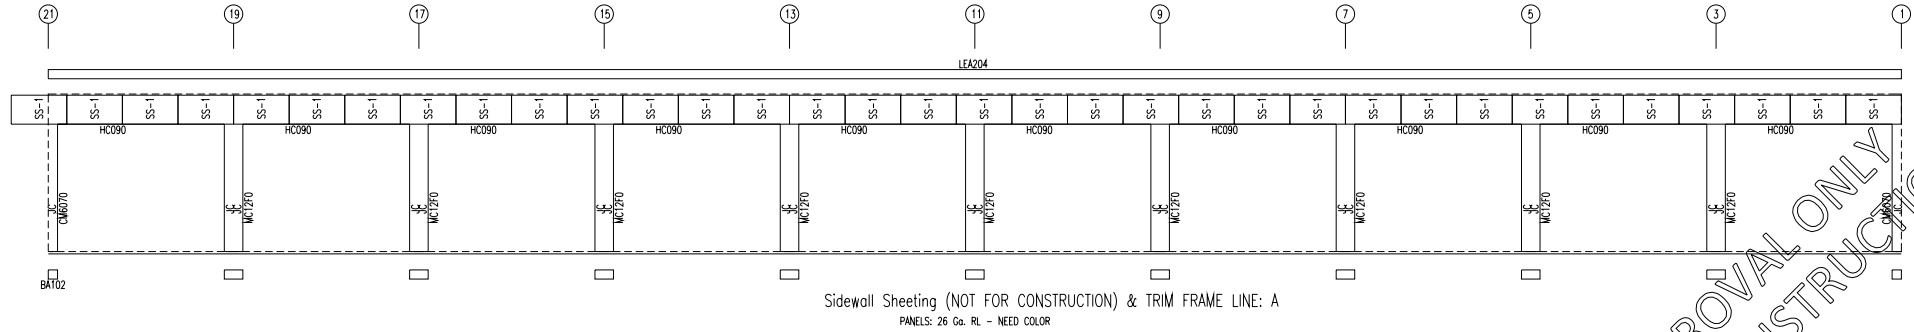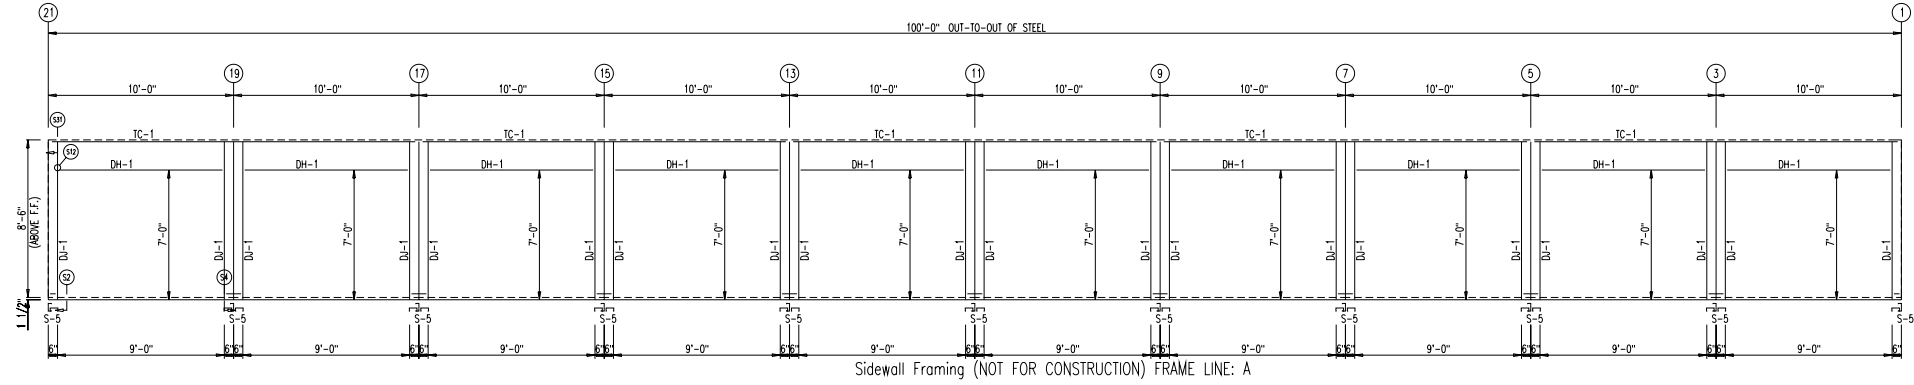

FOR APPROVAL ONLY
NOT FOR CONSTRUCTION


ROI Metal Buildings		PROJECT: BW62B699		April 2026	
423-991-0130		SIZE:		40.0 x 100.0 x 8.5	
		CITY:		Lenoir City	
		STATE:		TN	
JOB ID: 94097		APPROVAL		PRINTS ISSUED FOR	
Sheet		BY		DATE	
F2				6/12/26	

CONFIDENTIAL AND PROPRIETARY INFORMATION
THESE DRAWINGS ARE THE SOLE AND EXCLUSIVE PROPERTY OF THE BUILDING MANUFACTURER. SENSITIVE AND PROPRIETARY INFORMATION IS CONTAINED HEREIN. THESE DRAWINGS MAY ONLY BE USED FOR THE PROJECT AND SITE SPECIFICALLY IDENTIFIED HEREIN. UNAUTHORIZED REPRODUCTION OR USE OF THESE DRAWINGS MAY NOT BE USED TO CONSTRUCT THE BUILDING MANUFACTURER. THIS DOCUMENT AND ALL COPIES MUST BE RETURNED UPON DEMAND.

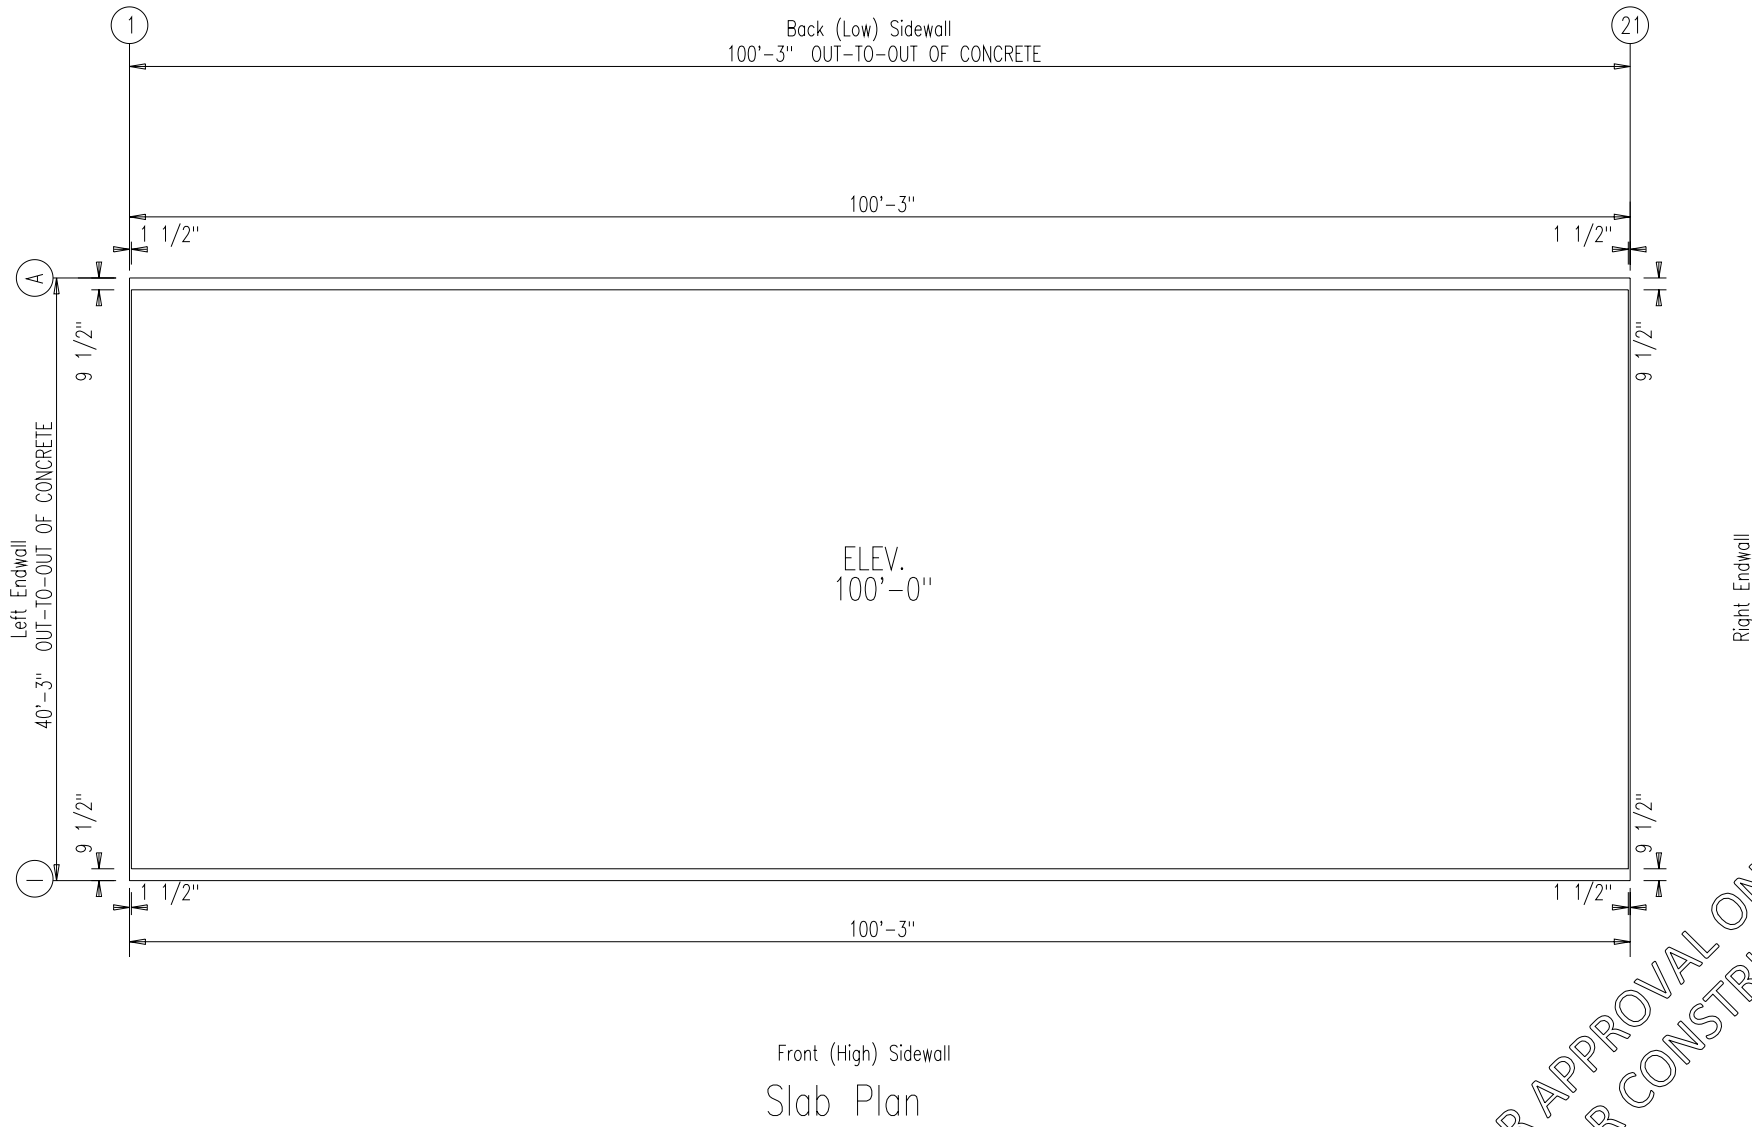

Front (High) Sidewall
Slab Plan

ROI Metal Buildings	PROJECT: BW625699 April 2026	CONFIDENTIAL AND PROPRIETARY INFORMATION	
423-991-0130	SIZE: 40.0 x 100.0 x 8.5	THESE DRAWINGS ARE THE SOLE AND EXCLUSIVE PROPERTY OF THE BUILDING MANUFACTURER. SENSITIVE AND PROPRIETARY INFORMATION IS CONTAINED HEREIN. THESE DRAWINGS MAY ONLY BE USED FOR THE PROJECT AND SITE SPECIFICALLY IDENTIFIED HEREIN. UNAUTHORIZED REPRODUCTION OR USE OF THESE DRAWINGS MAY NOT BE USED TO CONSTRUCT THE BUILDING MANUFACTURER. THIS DOCUMENT AND ALL COPIES MUST BE RETURNED UPON DEMAND.	
JOB ID: 94097	CITY: Lenoir City	APPROVAL	BY
Sheet	STATE: TN	PRINTS ISSUED FOR	DATE
E4			6/12/26

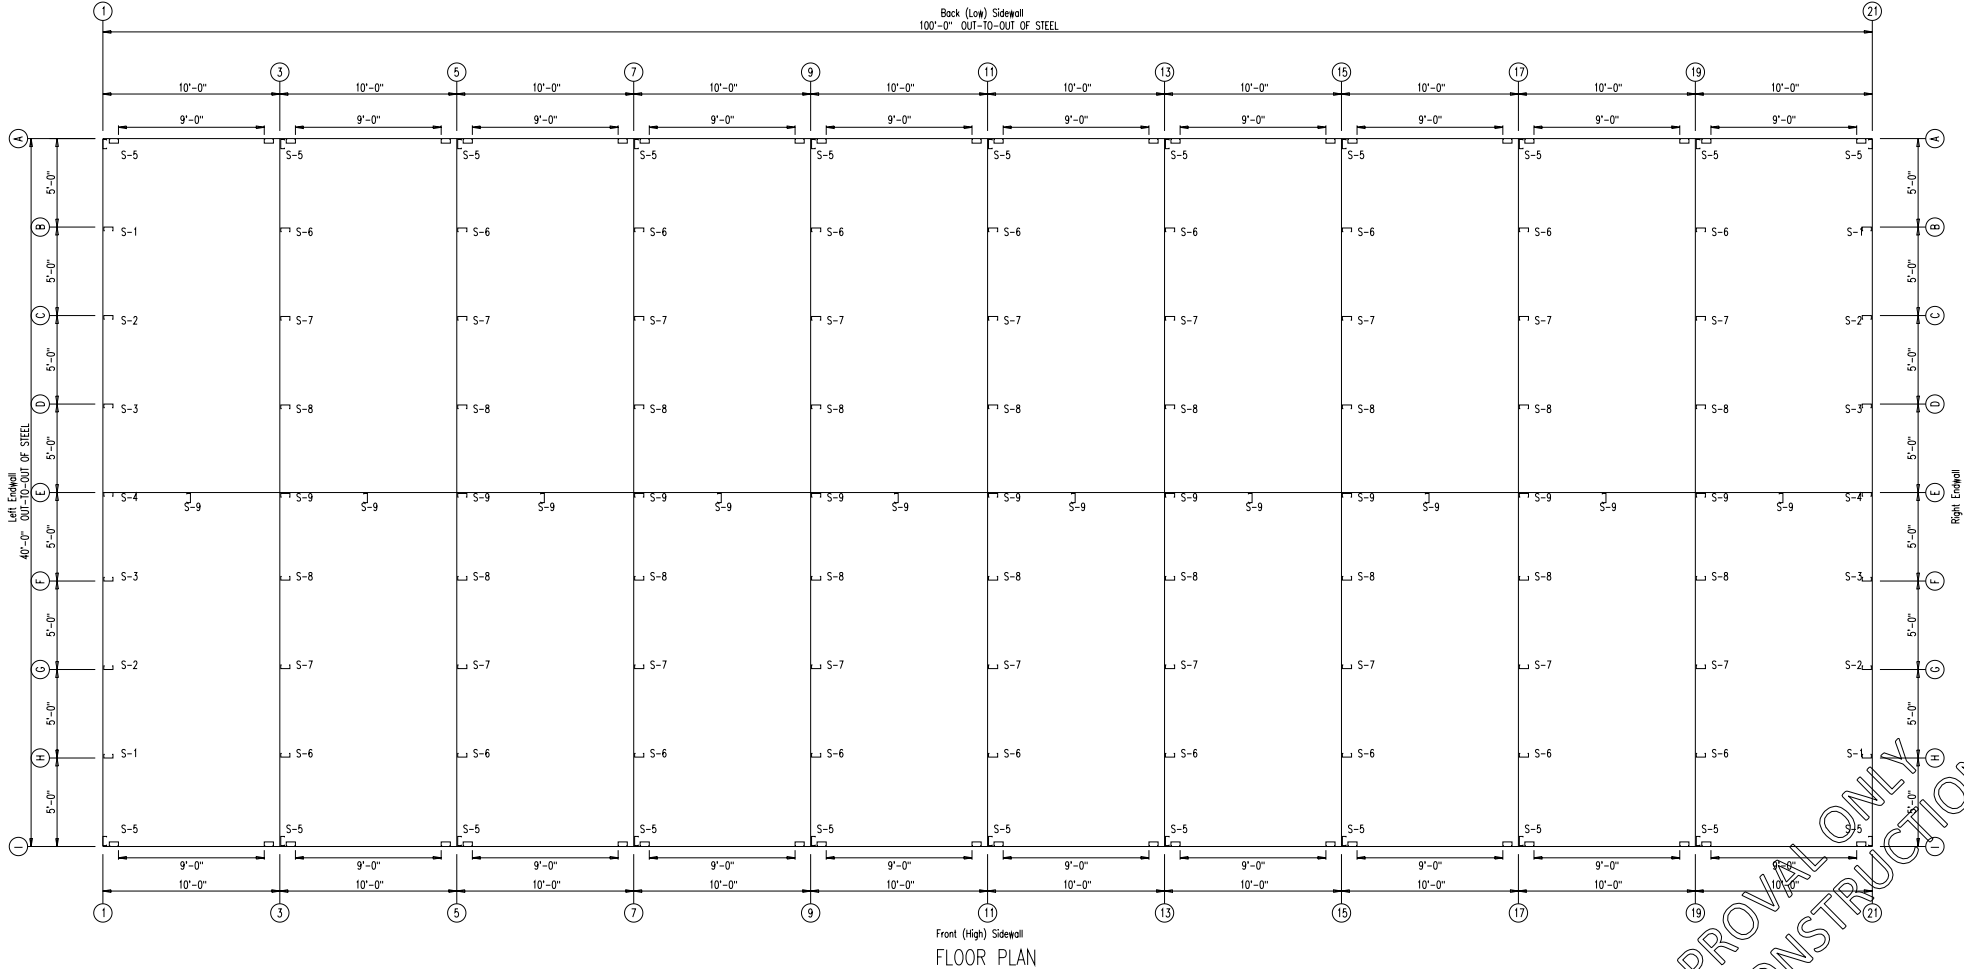

FLOOR PLAN

CONFIDENTIAL AND PROPRIETARY INFORMATION
THESE DRAWINGS ARE THE SOLE AND EXCLUSIVE PROPERTY OF THE BUILDING MANUFACTURER. NO PART OF THESE DRAWINGS MAY BE REPRODUCED OR TRANSMITTED IN ANY FORM OR BY ANY MEANS, ELECTRONIC OR MECHANICAL, WITHOUT THE WRITTEN PERMISSION OF THE BUILDING MANUFACTURER. UNAUTHORIZED PERSONS ARE STRICTLY PROHIBITED FROM USING THESE DRAWINGS FOR ANY PURPOSE OTHER THAN THE CONSTRUCTION OF THE BUILDING MANUFACTURED BY THE BUILDING MANUFACTURER. THIS DOCUMENT AND ALL COPIES MUST BE RETURNED UPON DEMAND.

PROJECT: B6699 April 2026
SIZE: 40.0 x 100.0 x 8.5
CITY: Lenoir City
STATE: TN


ROI Metal Buildings
423-991-0130

JOB ID: 94097

Sheet

F5

APPROVAL	PRINTS ISSUED FOR	BY	DATE
			6/12/26

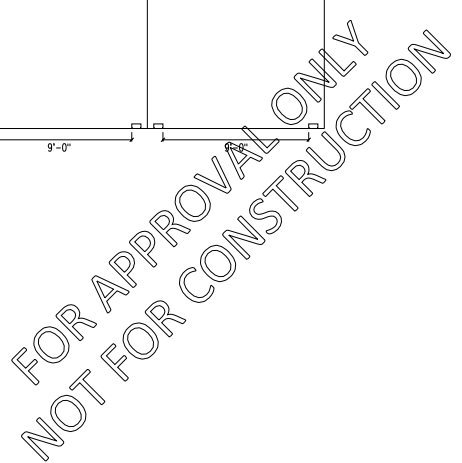

423-991-0130

Sheet

E6

STATE: TN

[illegible]

APPROVAL	6/12/26
ITS ISSUED FOR	DATE